

GAMBAR KERJA RUMAH TIPE 25 / 72 KAMAR LEBAR 2 METER



Perumahan

Bumi Karya Indah

PT. KARYATARUNA ADHIPRATAMA

Grha Satria, Jl. Sukahaji No. 126 Bandung 40152 Phone (022) 82006365 - 67

DAFTAR GAMBAR

NO	NO. LEMBAR	NAMA GAMBAR	KETERANGAN
1	A-A-03	ILUSTRASI BANGUNAN 3 DIMENSI	ARSITEKTURAL
2	A-01-04	DENAH	ARSITEKTURAL
3	A-02-05	TAMPAK	ARSITEKTURAL
4	A-03-06	POTONGAN	ARSITEKTURAL
5	A-03-07	POTONGAN	ARSITEKTURAL
6	A-04-08	DETAIL FASAD	ARSITEKTURAL
7	S-01-09	DETAIL CARPORT	STRUKTUR
8	S-02-10	DETAIL KUDA-KUDA	STRUKTUR
9	S-03-11	DETAIL PONDASI	STRUKTUR
10	A-05-12	DENAH POLA LANTAI	ARSITEKTURAL
11	A-06-13	DETAIL PLAFOND	ARSITEKTURAL
12	S-04-14	RENCANA ATAP	STRUKTUR
13	A-07-15	DENAH RENCANA KUSEN	ARSITEKTURAL
14	A-08-16	DETAIL KUSEN P1,P2 & P3	ARSITEKTURAL
15	A-09-17	DETAIL KUSEN JB 1 & BV	ARSITEKTURAL
16	A-10-18	DETAIL KUSEN JB 2	ARSITEKTURAL
17	S-05-19	DETAIL TOILET	STRUKTUR
18	S-06-20	DETAIL DAPUR	STRUKTUR
19	S-07-21	SKEMA STRUKTUR	STRUKTUR
20	S-08-22	SKEMA STRUKTUR	STRUKTUR
21	ME-01-23	SKEMA ELEKTRIKAL	MEKANIKAL/ELEKTRIKAL
22	ME-02-24	SKEMA JALUR AIR	MEKANIKAL/ELEKTRIKAL



A ILUSTRASI BANGUNAN 3 DIMENSI
A-A-03 NTS

CATATAN :

KETERANGAN

DEVELOPER



PT. KARYATARUNA ADHIPRATAMA
REAL ESTATE & DEVELOPER
Jalan Sukahaji No.126 Bandung 40152
Telp: (022) 82006365, 82006367 Fax: (022) 82006362

PROYEK

BUMI KARYA INDAH

GAMBAR

**ILUSTRASI BANGUNAN
3 DIMENSI**

TYPE 25/72 (25.2)

DIRENCANAKAN DAN DIGAMBAR:

PURNAMA KUSUMA MAHBUB

DIPERIKSA:


RANI SHINTA HAPSARI

DISETUJUI :

AGNES STEPHANIA A. T.

NO. REVISI	TANGGAL
01.	
02.	
NOMOR LEMBAR	JUMLAH LEMBAR

A-A-03 **24**

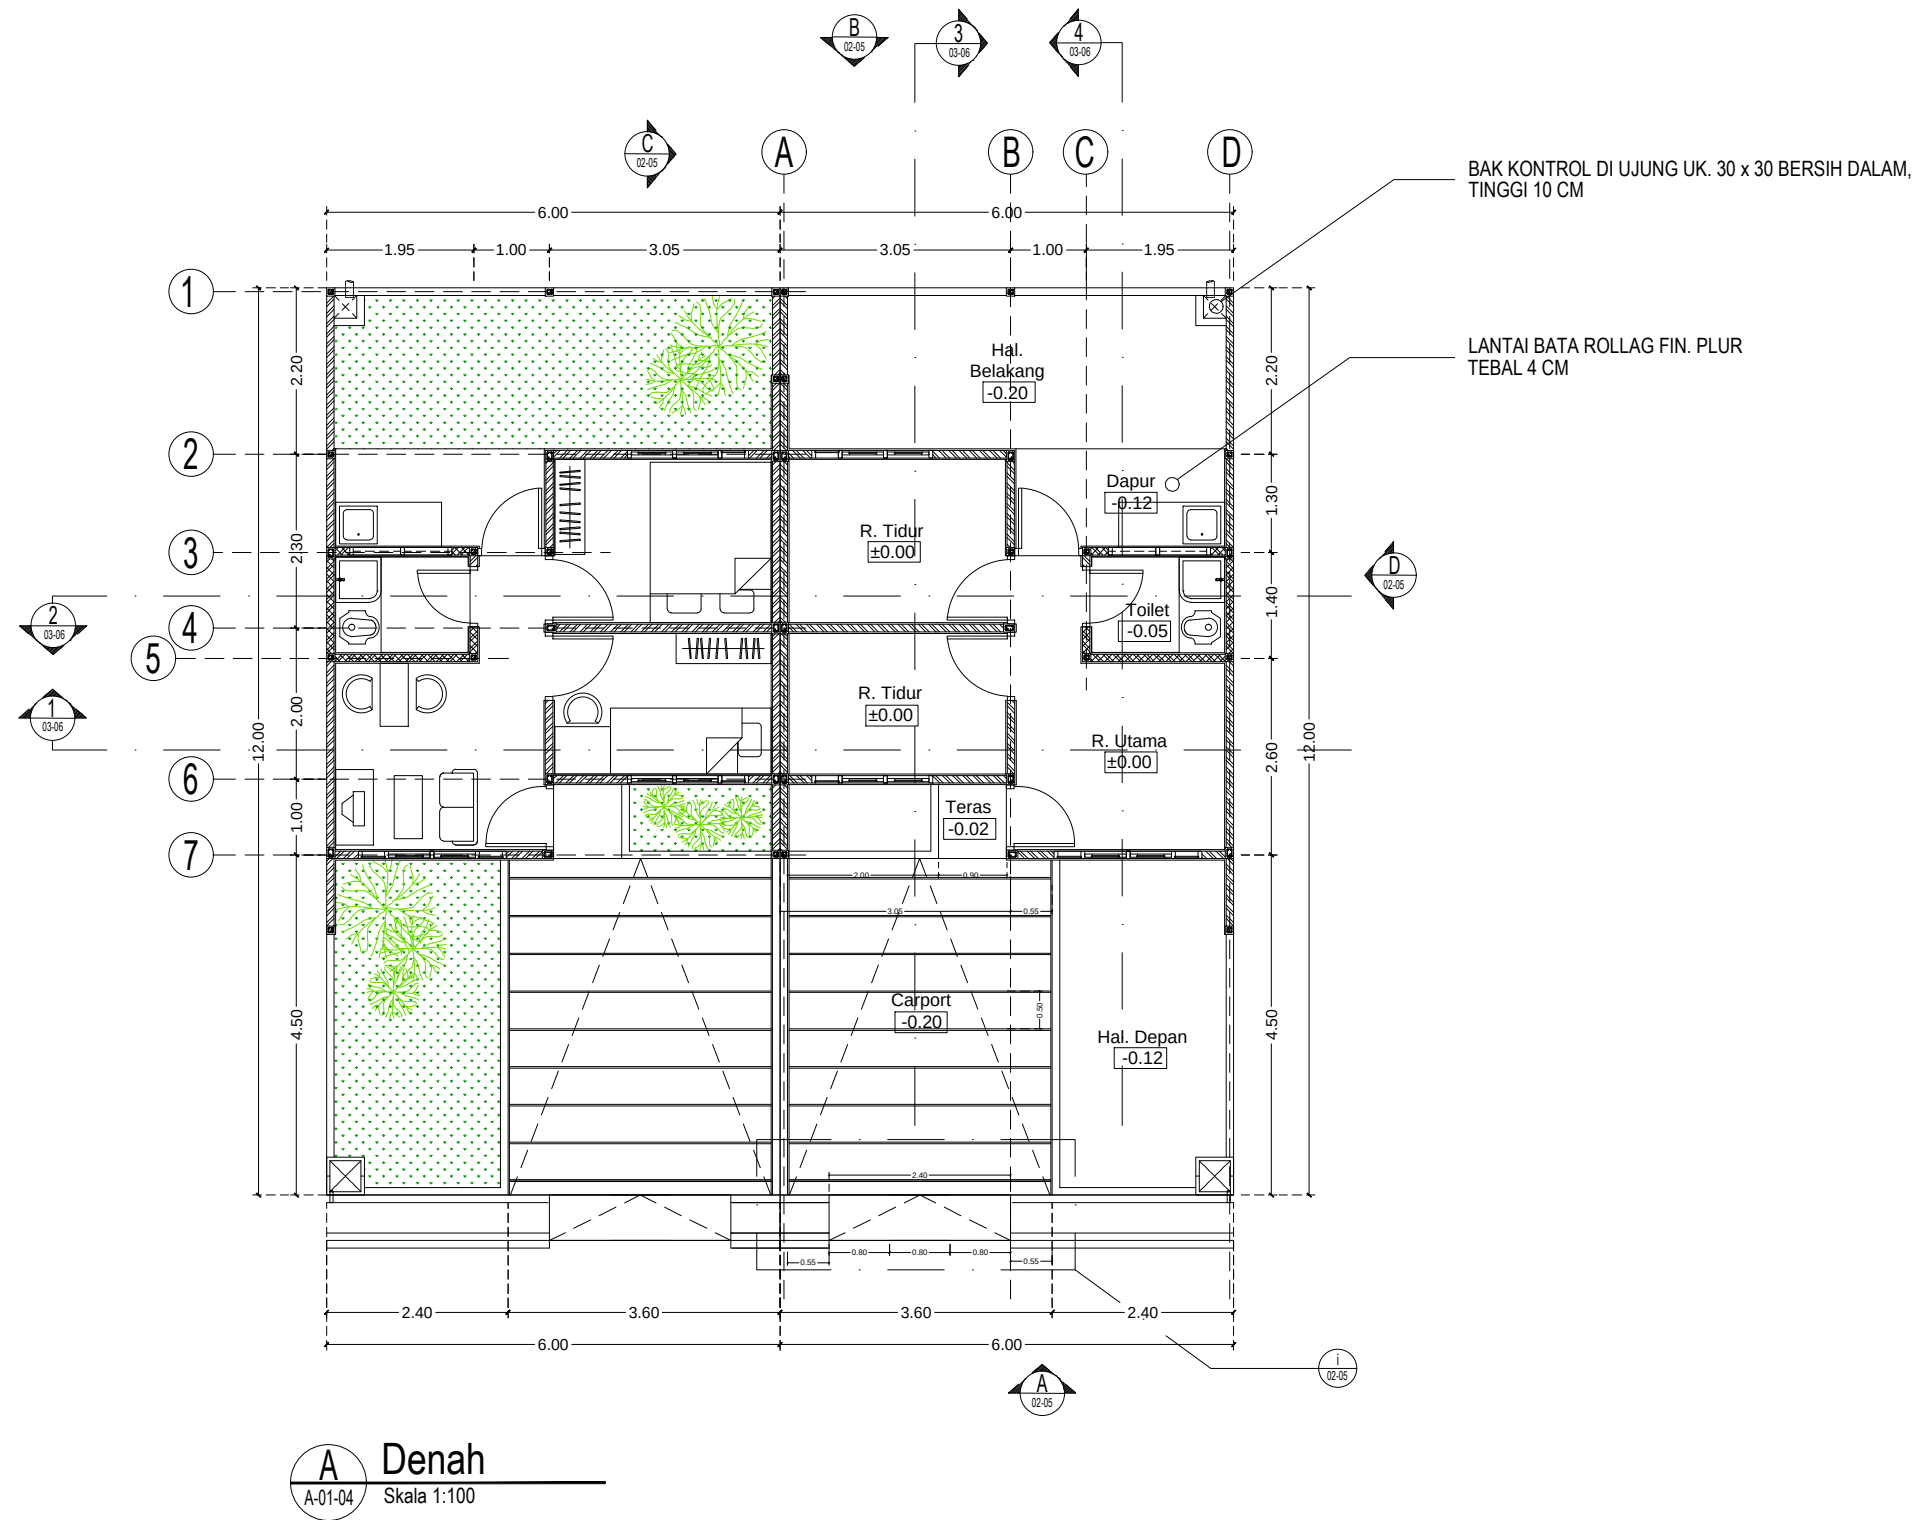

CATATAN :

KETERANGAN

DEVELOPER



PT. KARYATARUNA ADHIPRATAMA
REAL ESTATE & DEVELOPER
Jalan Sukahaji No.126 Bandung 40152
Telp: (022) 82006365, 82006367 Fax: (022) 82006362

PROYEK

BUMI KARYA INDAH

GAMBAR

DENAH

TYPE 25/72 (25.2)

DIRENCANAKAN DAN DIGAMBAR:

PURNAMA KUSUMA MAHBUB

DIPERIKSA:

RANI SHINTA HAPSARI

DISETUJUI :

AGNES STEPHANIA A. T.


NO. REVISI	TANGGAL
01.	
02.	
NOMOR LEMBAR	JUMLAH LEMBAR

A-01-04


24

002_PL-BKI/EX/2572-2/ASDIR/VI/2022


20/06/2022

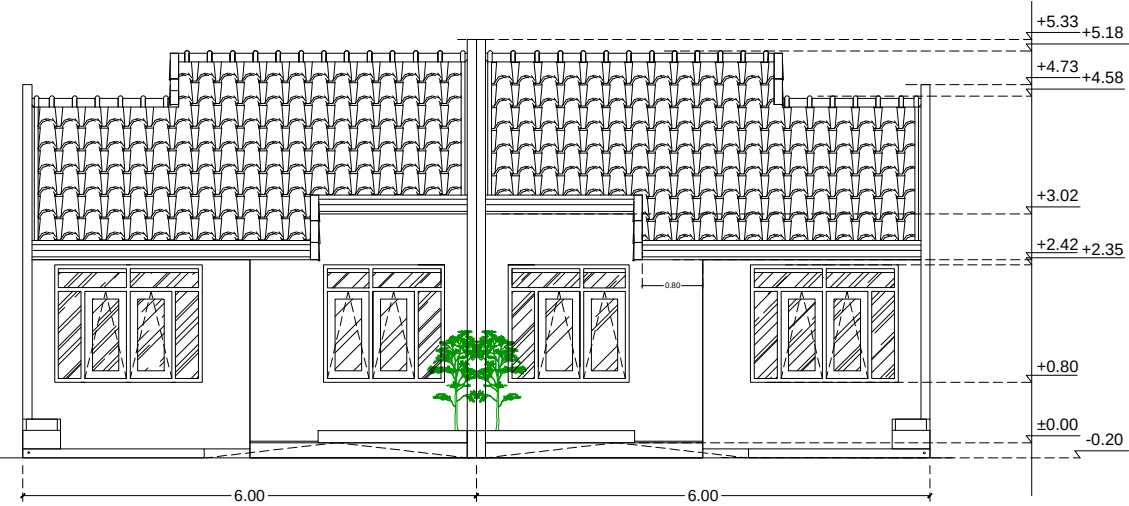


A Tampak - A
A-02-05 Skala 1:100

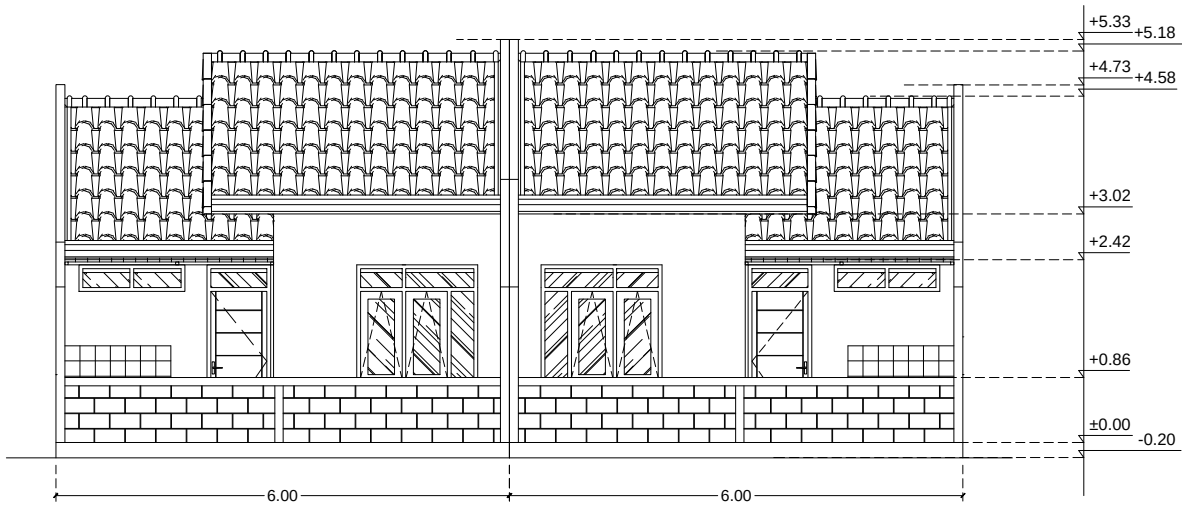

A Tampak - B
A-02-05 Skala 1:100

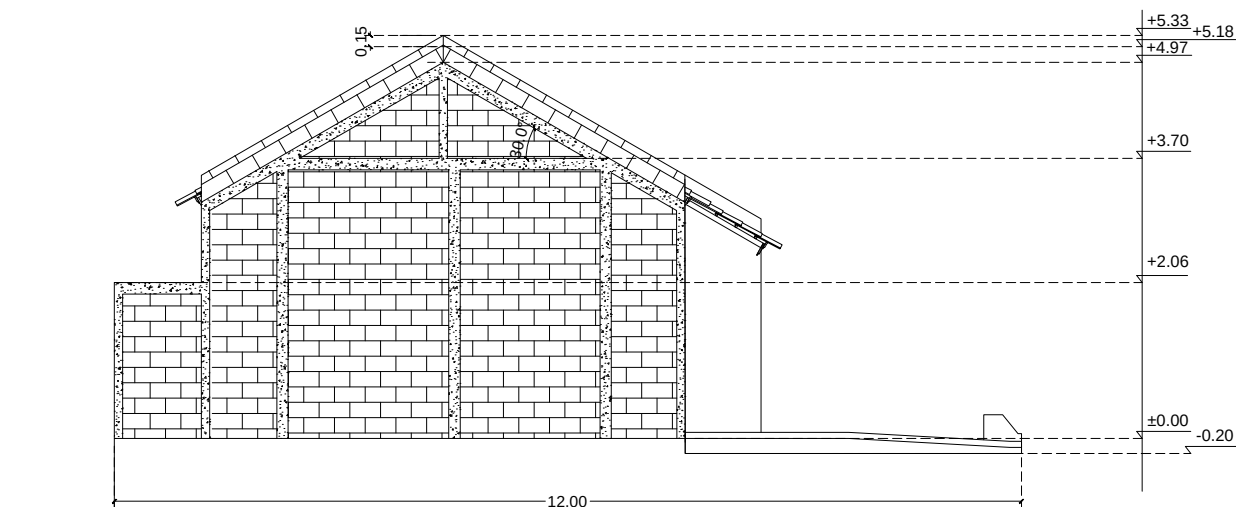


A Tampak - C
A-02-05 Skala 1:100

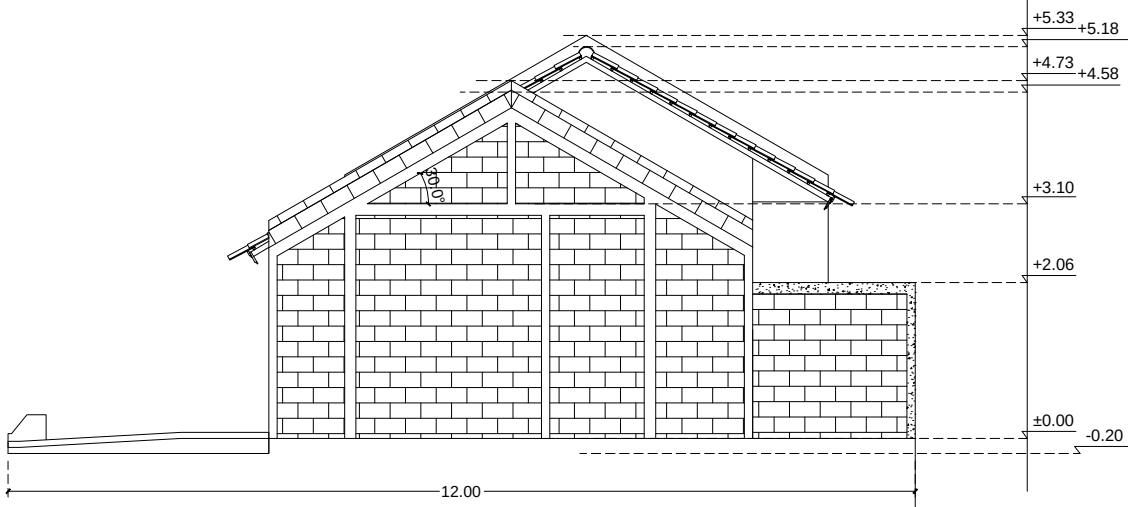

A Tampak - D
A-02-05 Skala 1:100

CATATAN :

KETERANGAN

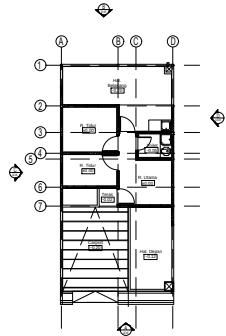

DEVELOPER



PT. KARYATARUNA ADHIPRATAMA
REAL ESTATE & DEVELOPER
Jalan Sukahaji No.126 Bandung 40152
Telp: (022) 82006365, 82006367 Fax: (022) 82006362

PROYEK

BUMI KARYA INDAH

GAMBAR

TAMPAK

TYPE 25/72 (25.2)

DIRENCANAKAN DAN DIGAMBAR:

PURNAMA KUSUMA MAHBUB

DIPERIKSA:

RANI SHINTA HAPSARI

DISETUJUI :

AGNES STEPHANIA A. T.


NO. REVISI	TANGGAL
01.	
02.	
NOMOR LEMBAR	JUMLAH LEMBAR

A-02-05


24

002_PL-BKI/EX/2572-2/ASDIR/VI/2022

20/06/2022

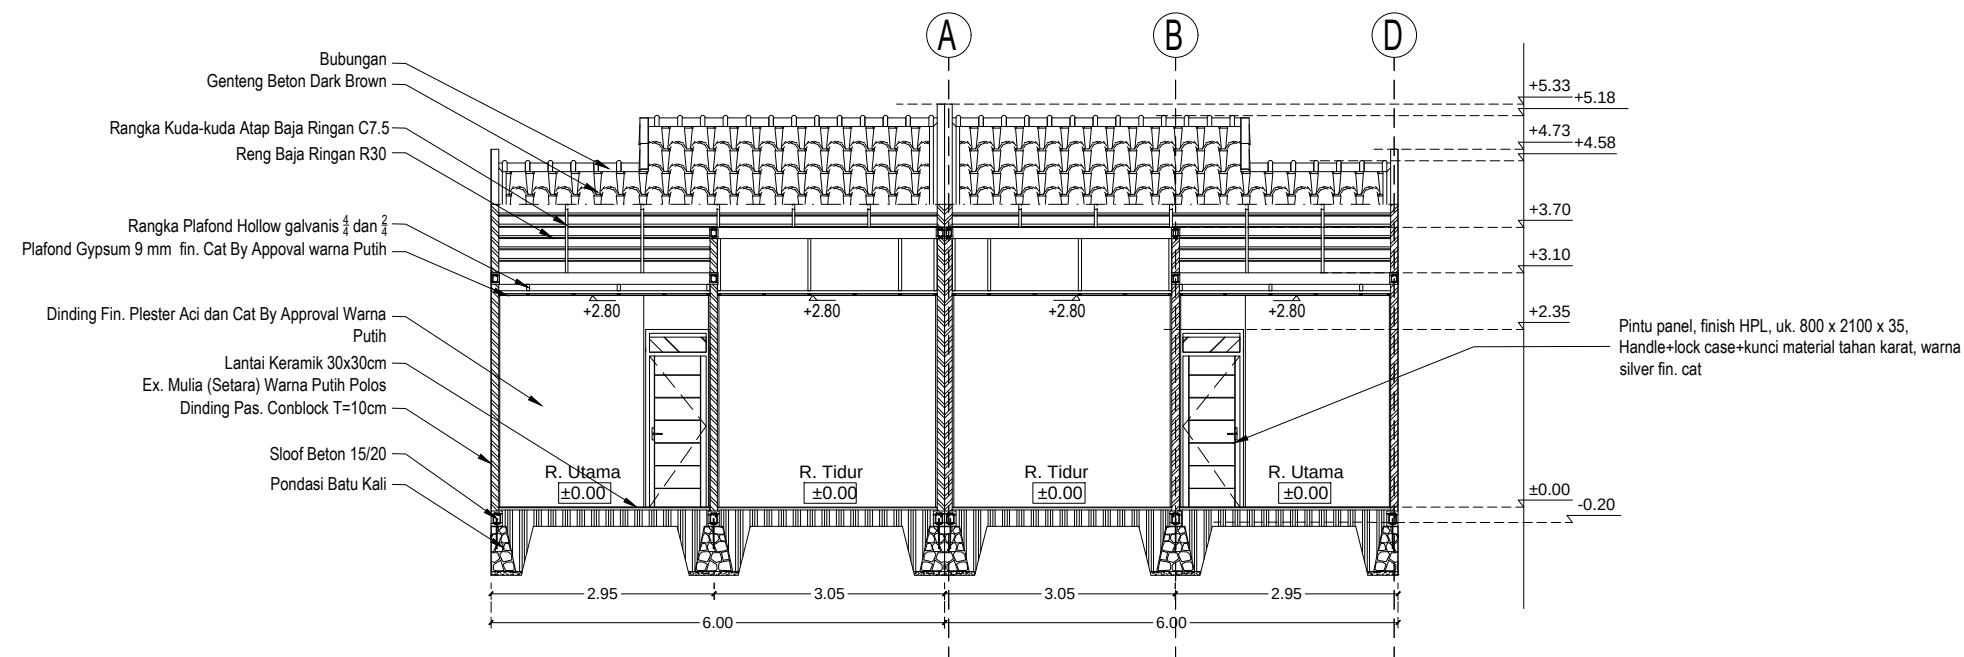

A Potongan - 1
A-03-06 Skala 1:100

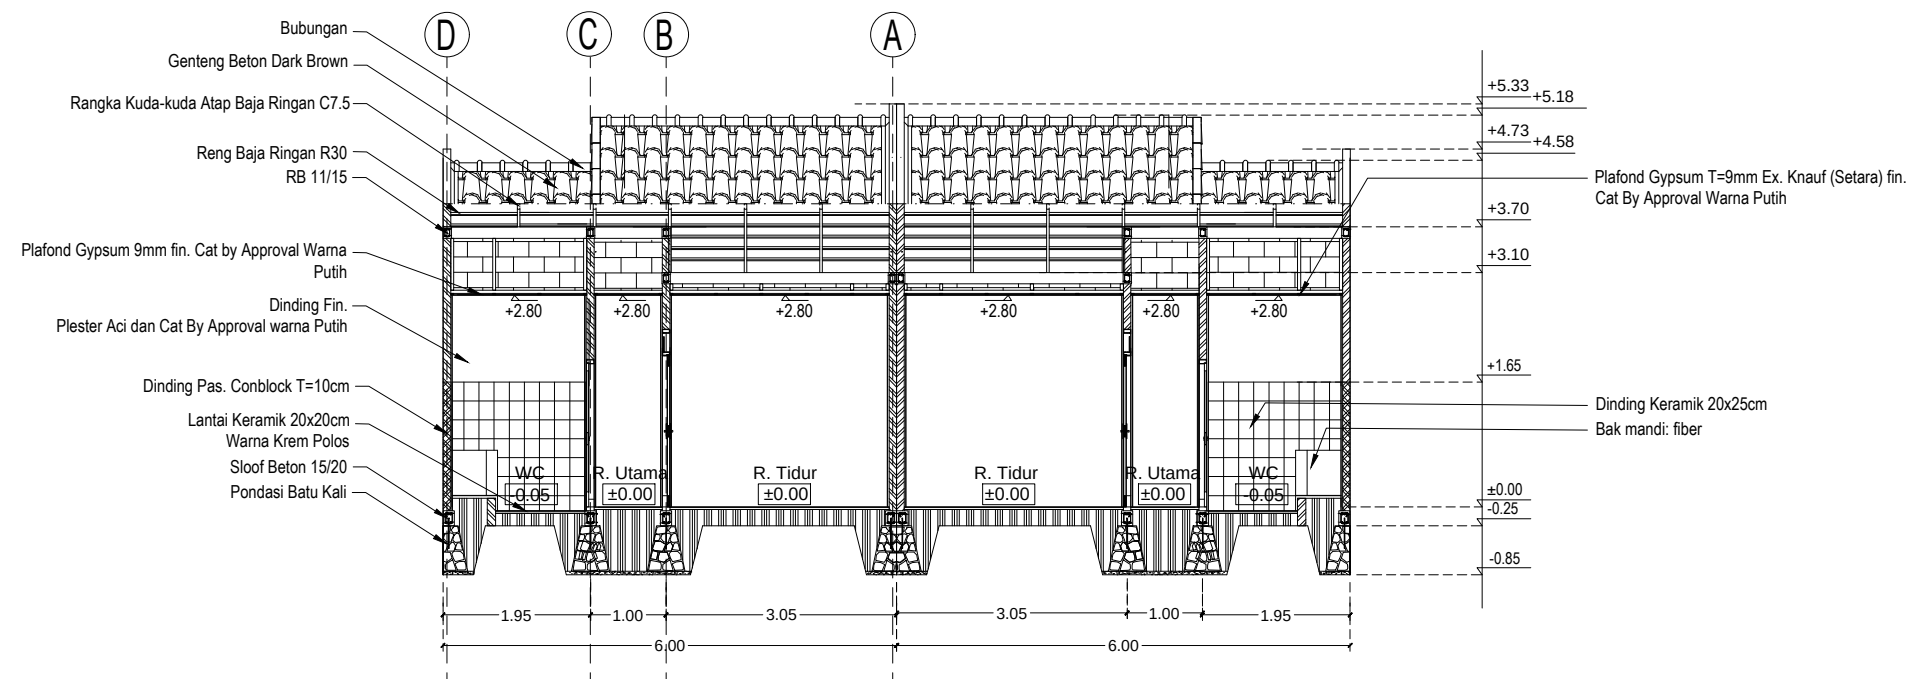


A Potongan - 2
A-03-06 Skala 1:100

CATATAN :

- JUMLAH PASANGAN CONBLOCK
= 15 LAYER DARI ATAS SLOOF
SAMPAI DENGAN BAWAH RING
BALK

KETERANGAN

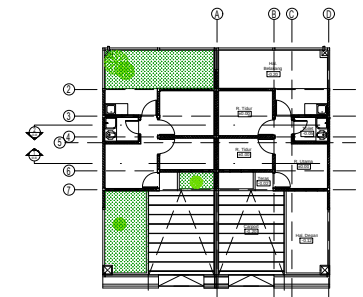

DEVELOPER



PT. KARYATARUNA ADHIPRATAMA
REAL ESTATE & DEVELOPER
Jalan Sukahaji No.126 Bandung 40152
Telp: (022) 82006365, 82006367 Fax: (022) 82006362

PROYEK

BUMI KARYA INDAH

GAMBAR

POTONGAN

TYPE 25/72 (25.2)

DIRENCANAKAN DAN DIGAMBAR:

PURNAMA KUSUMA MAHBUB

DIPERIKSA:

RANI SHINTA HAPSARI

DISETUJUI :

AGNES STEPHANIA A. T.


NO. REVISI	TANGGAL
01.	
02.	
NOMOR LEMBAR	JUMLAH LEMBAR

A-03-06


24

002_PL-BKI/EX/2572-2/ASDIR/VI/2022

20/06/2022

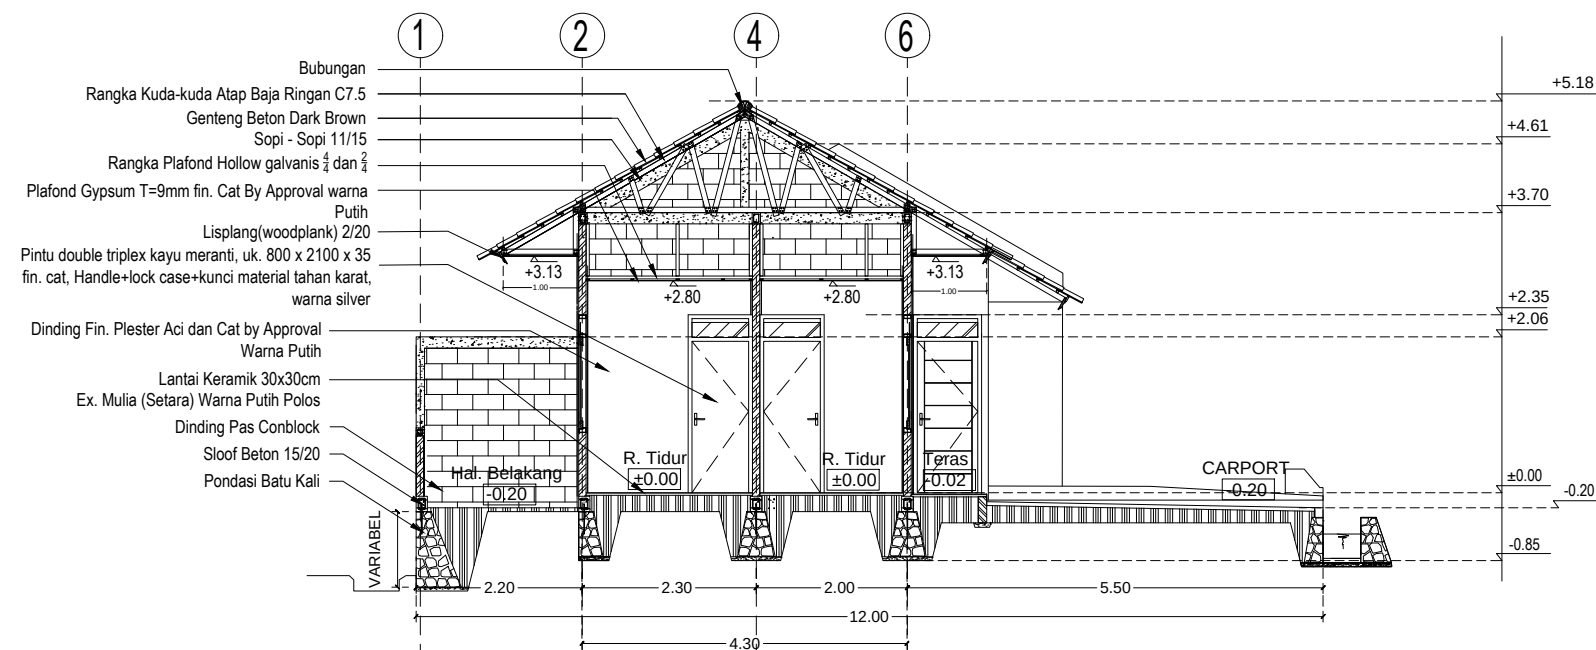


A Potongan - 3
A-03-07 Skala 1:100

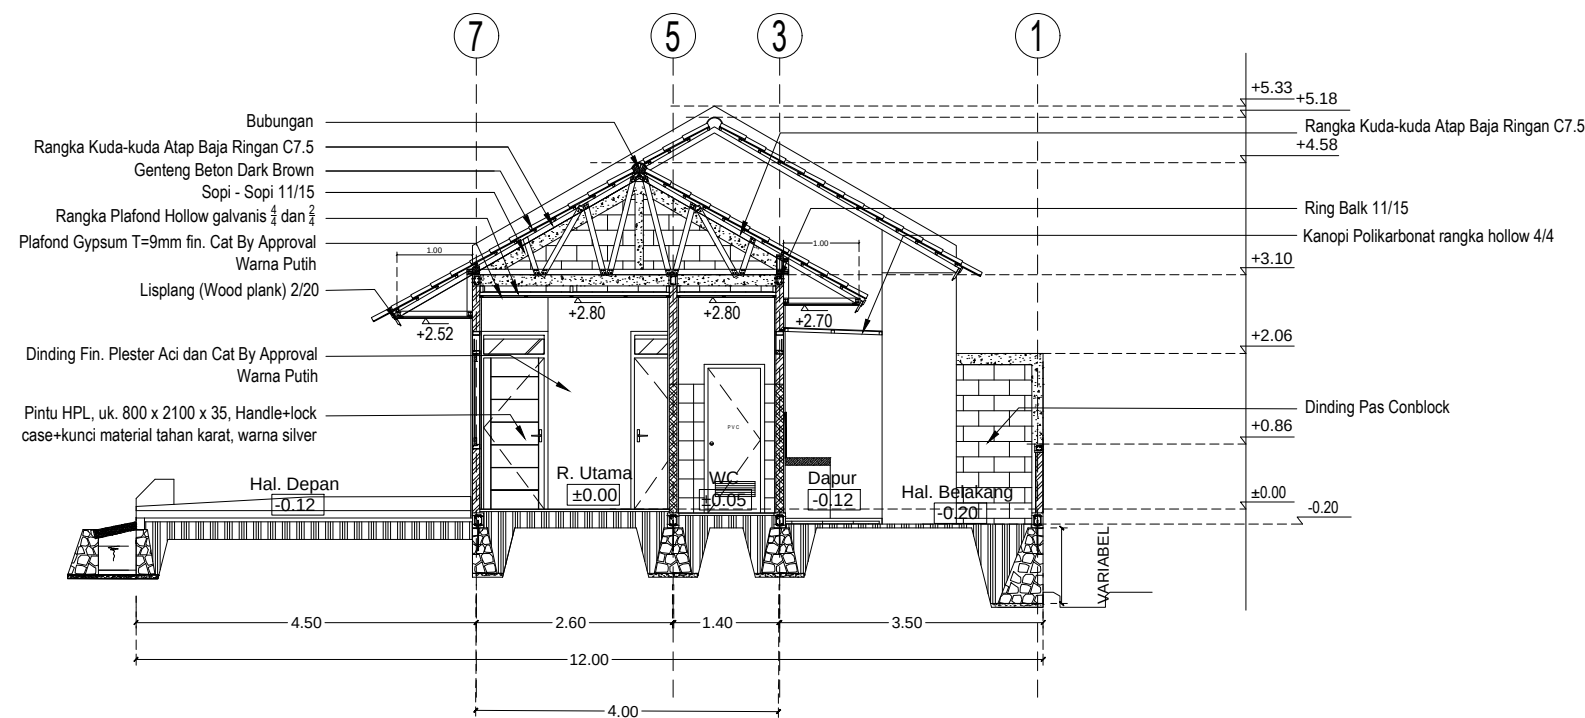

A Potongan - 4
A-03-07 Skala 1:100

CATATAN :

KETERANGAN

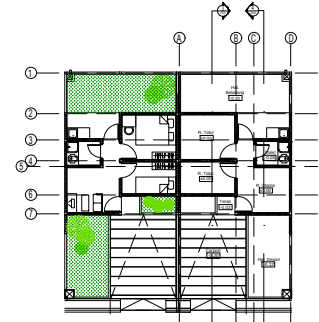

DEVELOPER



PT. KARYATARUNA ADHIPRATAMA
REAL ESTATE & DEVELOPER
Jalan Sukahaji No.126 Bandung 40152
Telp: (022) 82006365, 82006367 Fax: (022) 82006362

PROYEK

BUMI KARYA INDAH

GAMBAR

POTONGAN

TYPE 25/72 (25.2)

DIRENCANAKAN DAN DIGAMBAR:

PURNAMA KUSUMA MAHBUB

DIPERIKSA:

RANI SHINTA HAPSARI

DISETUJUI :

AGNES STEPHANIA A. T.

NO. REVISI	TANGGAL
01.	
02.	
NOMOR LEMBAR	JUMLAH LEMBAR

A-03-07

24

002_PL-BKI/EX/2572-2/ASDIR/VI/2022

20/06/2022

CATATAN :

KEY PLAN

DEVELOPER



PT. KARYATARUNA ADHIPRATAMA
REAL ESTATE & DEVELOPER
Jalan Sukahaji No. 128 Bandung 40152
Telp: (022) 82006365, 82006367 Fax: (022) 82006362

PROYEK

BUMI KARYA INDAH

GAMBAR

DETAIL FASAD

TYPE 25/72 (25.2)

DIRENCANAKAN dan DIGAMBAR :

PURNAMA_KUSUMA_MAHBUB

DIPERIKSA:

RANI_SHINTA_HAPSARI

DISETUJUI :

AGNES STEPHANIA A. T.

NO. REVISI

TANGGAL

01.


02.

NOMOR LEMBAR

JUMLAH LEMBAR

A-04-08

24

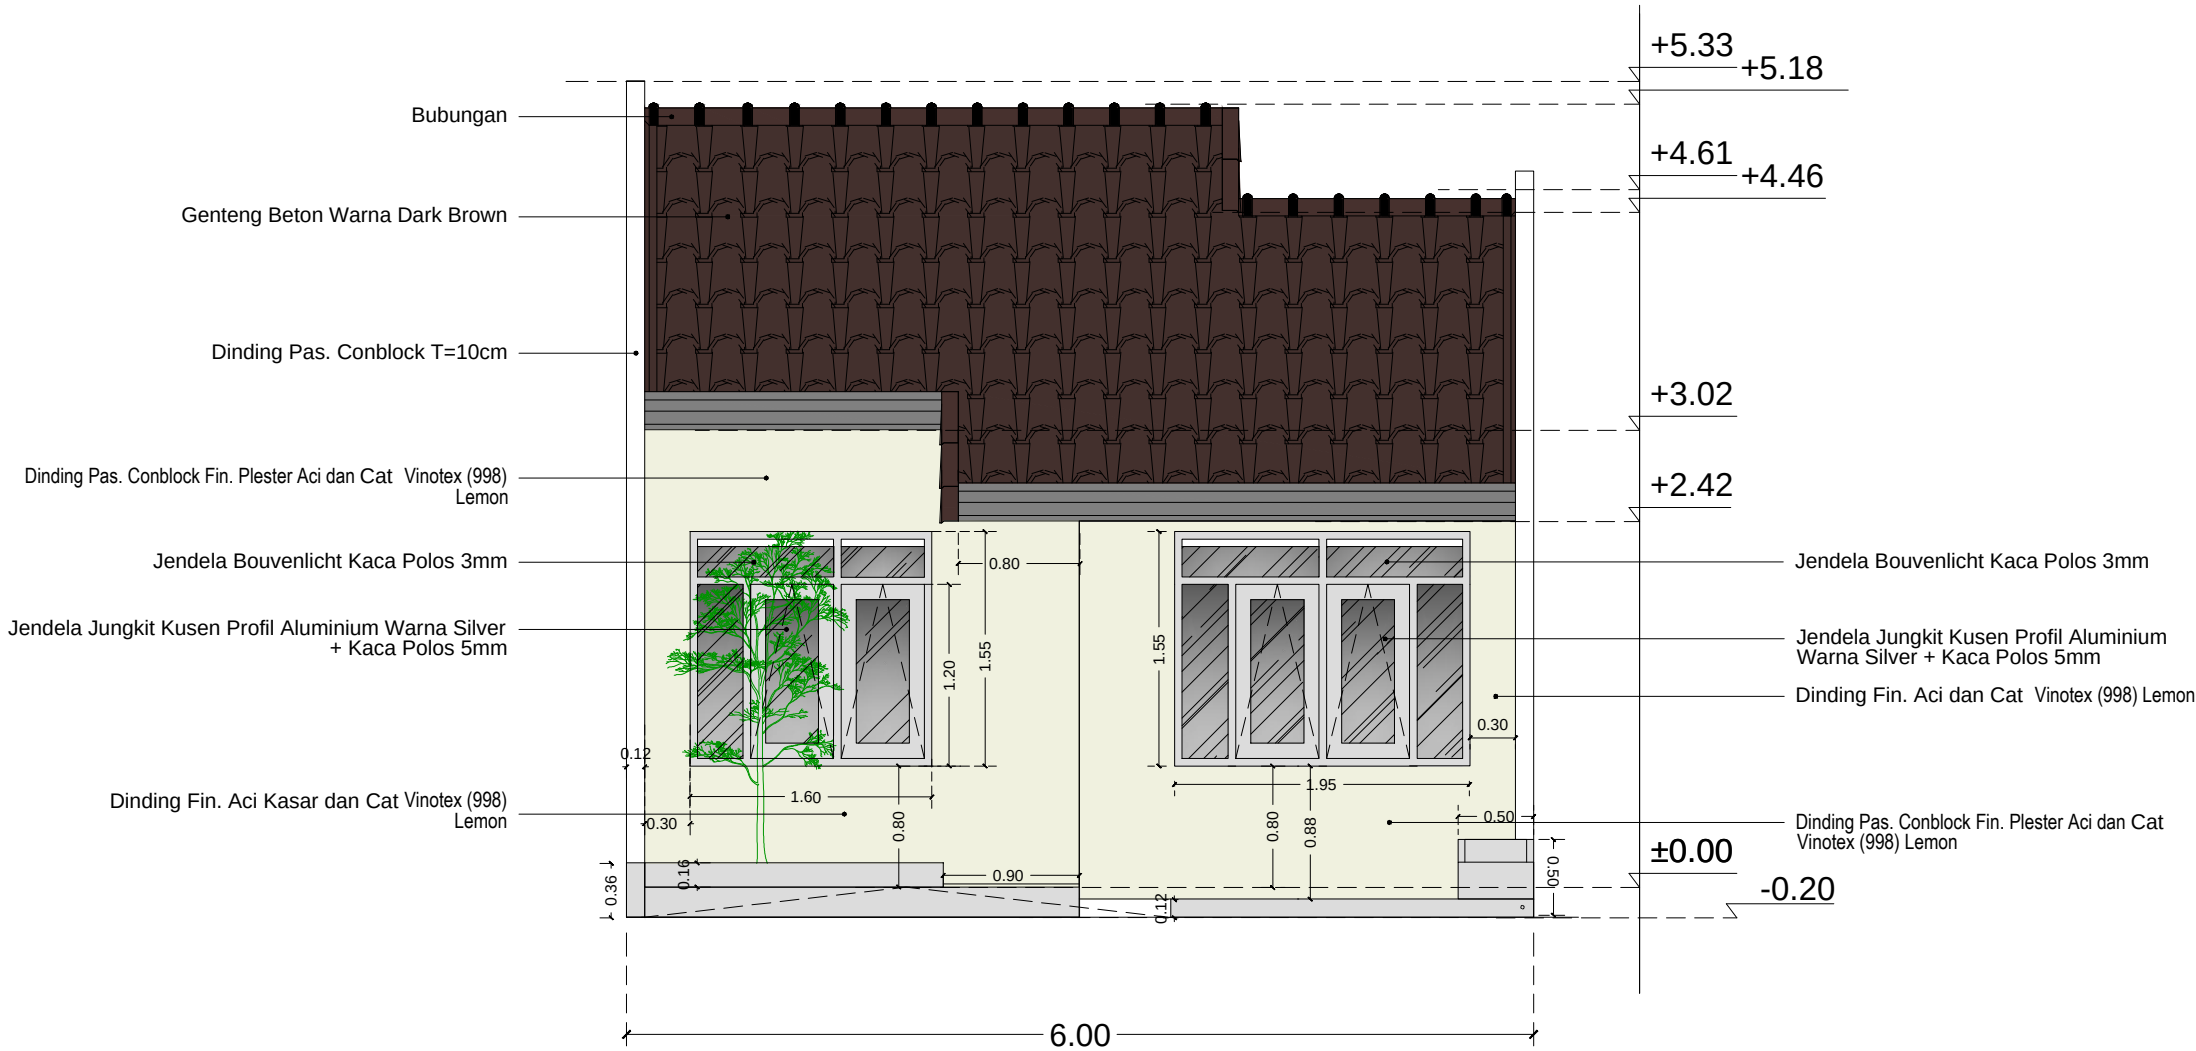


DETAIL Tampak A

Skala 1 : 50

002_PL-BKI/EX/2572-2/ASDIR/VI/2022

20/06/2022

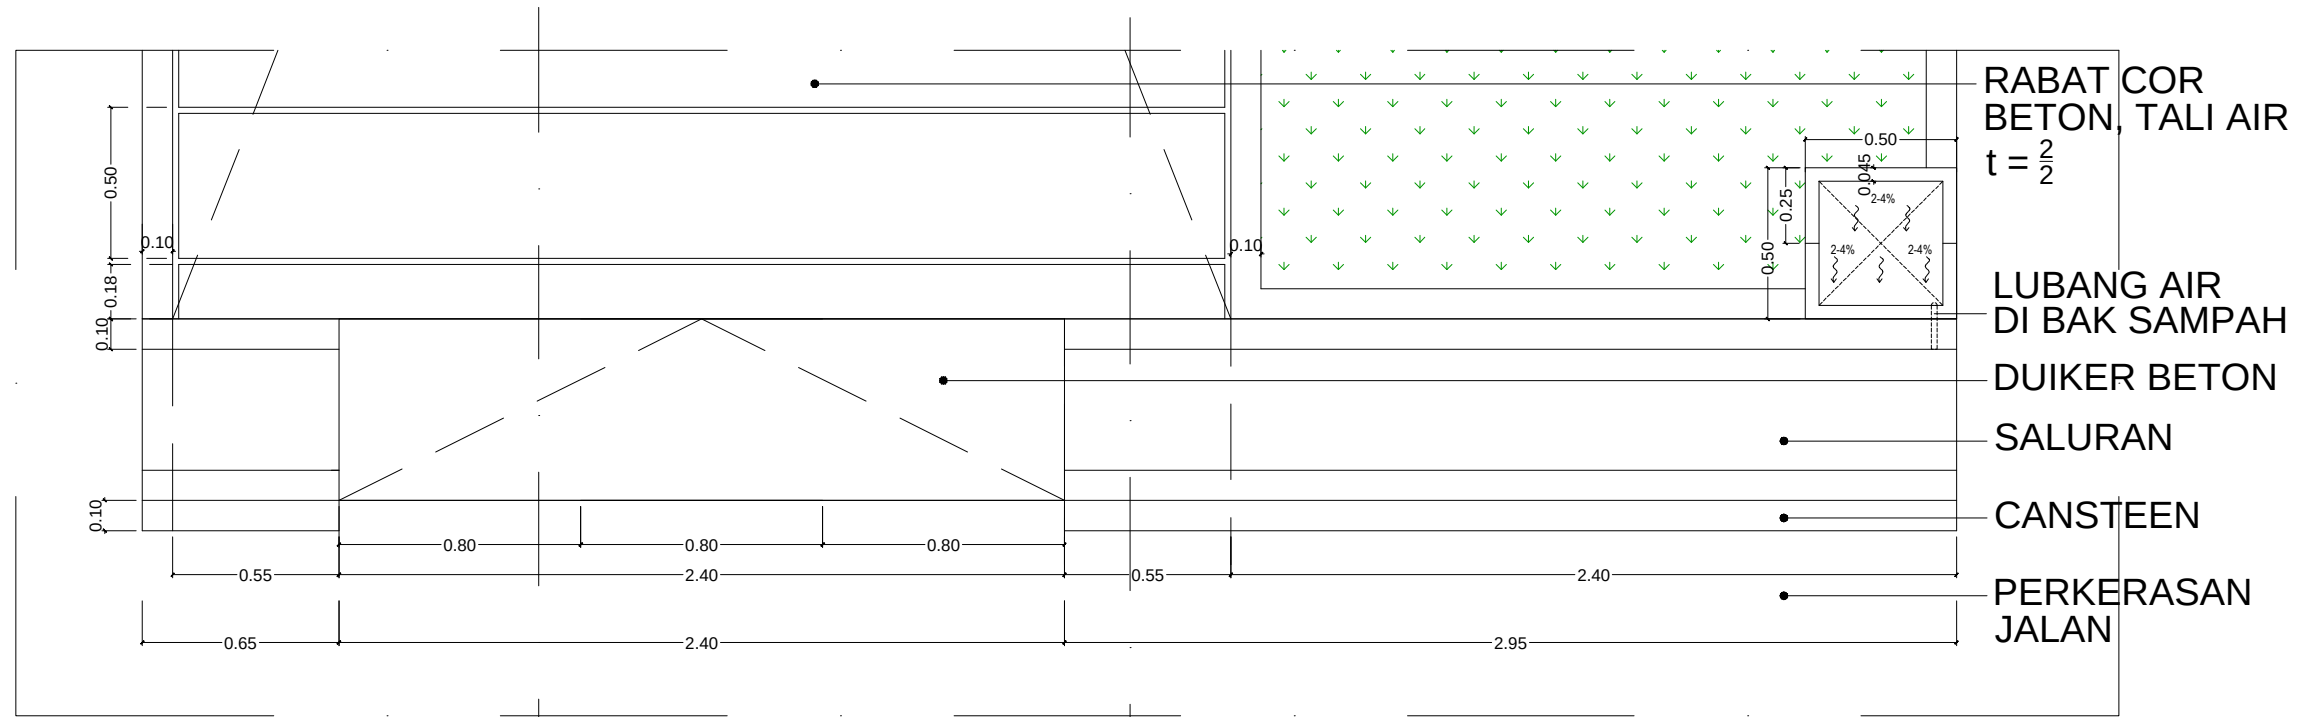


DETAIL CARPORT

Skala 1:20

1

2

BATAS KAVLING

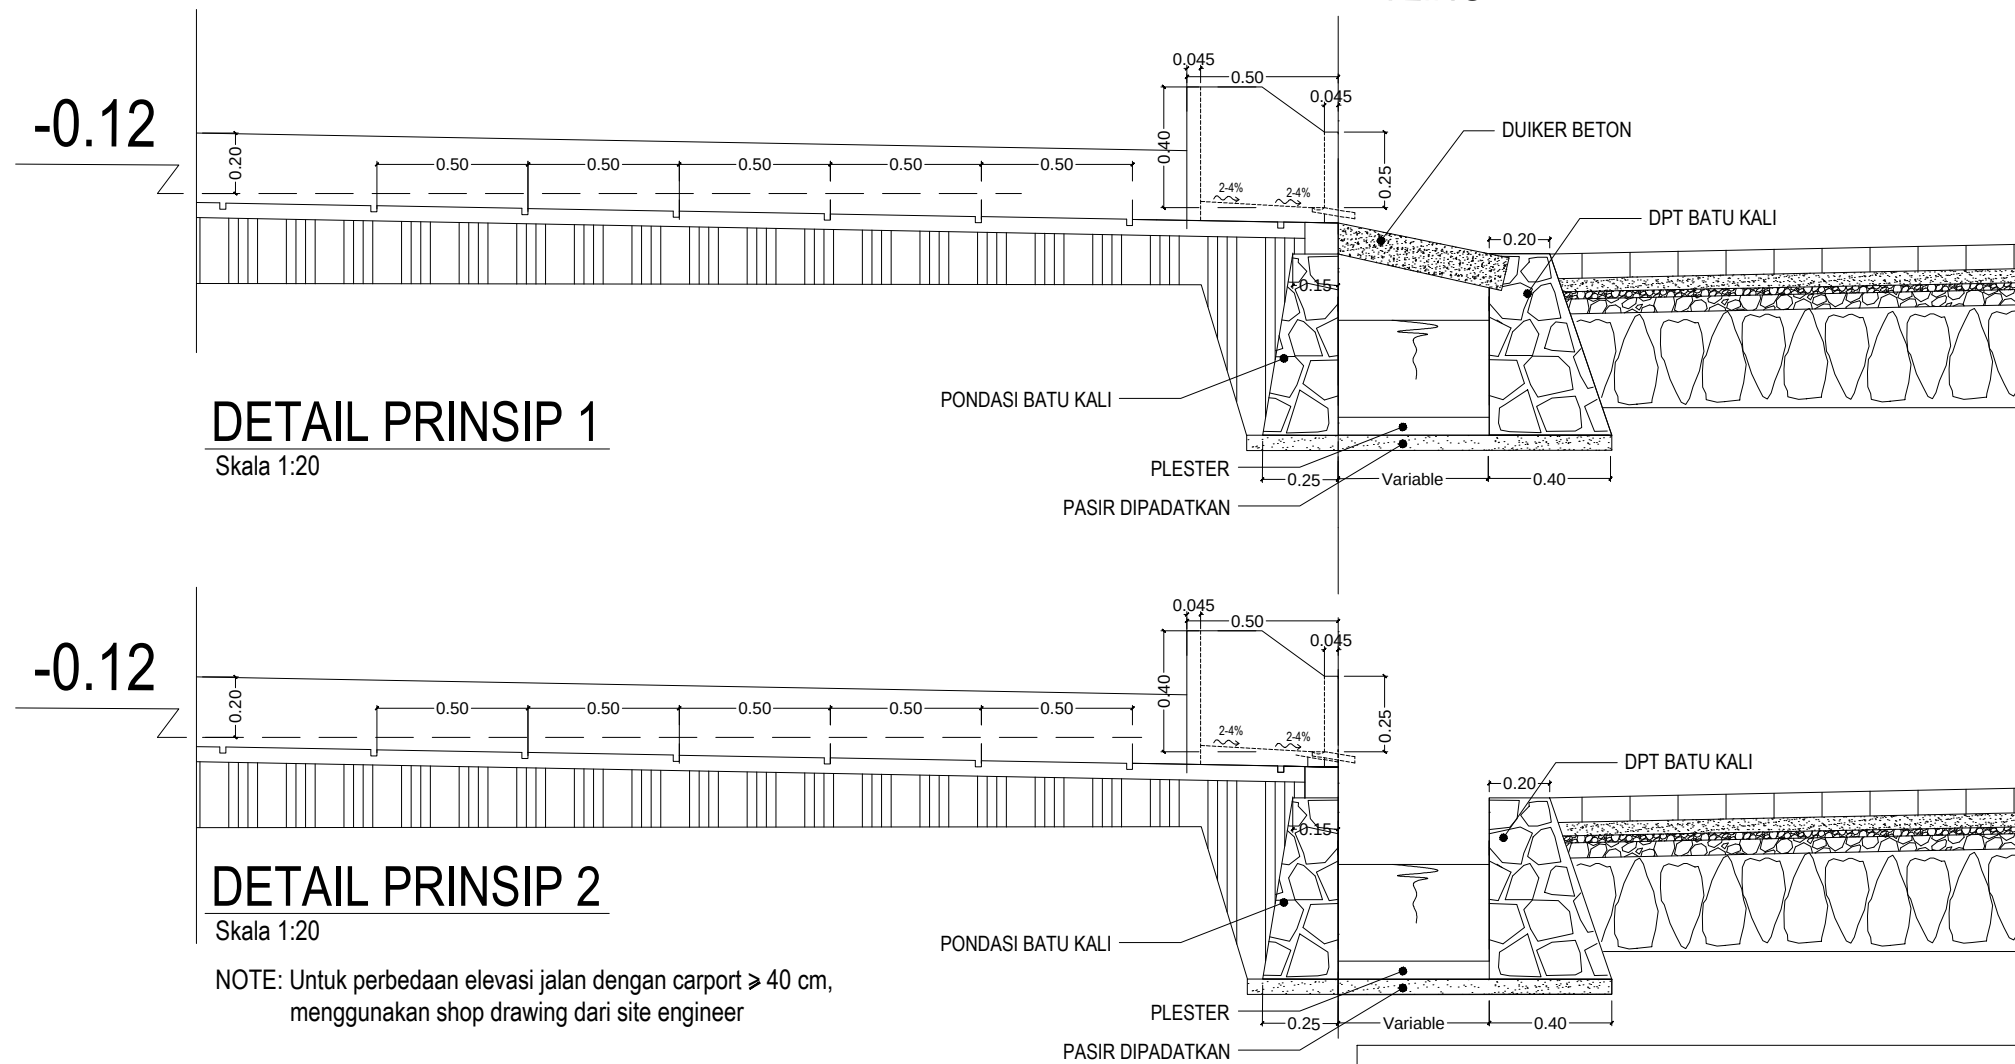

DETAIL PRINSIP 1

Skala 1:20

DETAIL PRINSIP 2


Skala 1:20

NOTE: Untuk perbedaan elevasi jalan dengan carport ≥ 40 cm, menggunakan shop drawing dari site engineer

CATATAN :

- Untuk Kavling - kavling di Jalan jalan sekunder dan boulevard : duiker 3 buah uk. 80 cm (ROW 8,10,12)
- Untuk Kavling - kavling di Jalan jalan lingkungan : duiker 2 buah uk. 80 cm (ROW 6,7)

KETERANGAN

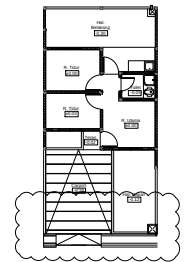

DEVELOPER



PT. KARYATARUNA ADHIPRATAMA
REAL ESTATE & DEVELOPER
Jalan Sukahaji No.126 Bandung 40152
Telp: (022) 82006365, 82006367 Fax: (022) 82006362

PROYEK

BUMI KARYA INDAH

GAMBAR

DETAIL CARPORT

TYPE 25/72 (25.2)

SKALA 1:50

DIRENCANAKAN dan DIGAMBAR :

PURNAMA KUSUMA MAHBUB

DIPERIKSA:

RANI SHINTA HAPSARI

DISETUJUI :

AGNES STEPHANIA A. T.

NO. REVISI

TANGGAL

01.

NOMOR LEMBAR


JUMLAH LEMBAR

S-01-9

24


002_PL-BKI/EX/2572-2/ASDIR/VI/2022

20/06/2022

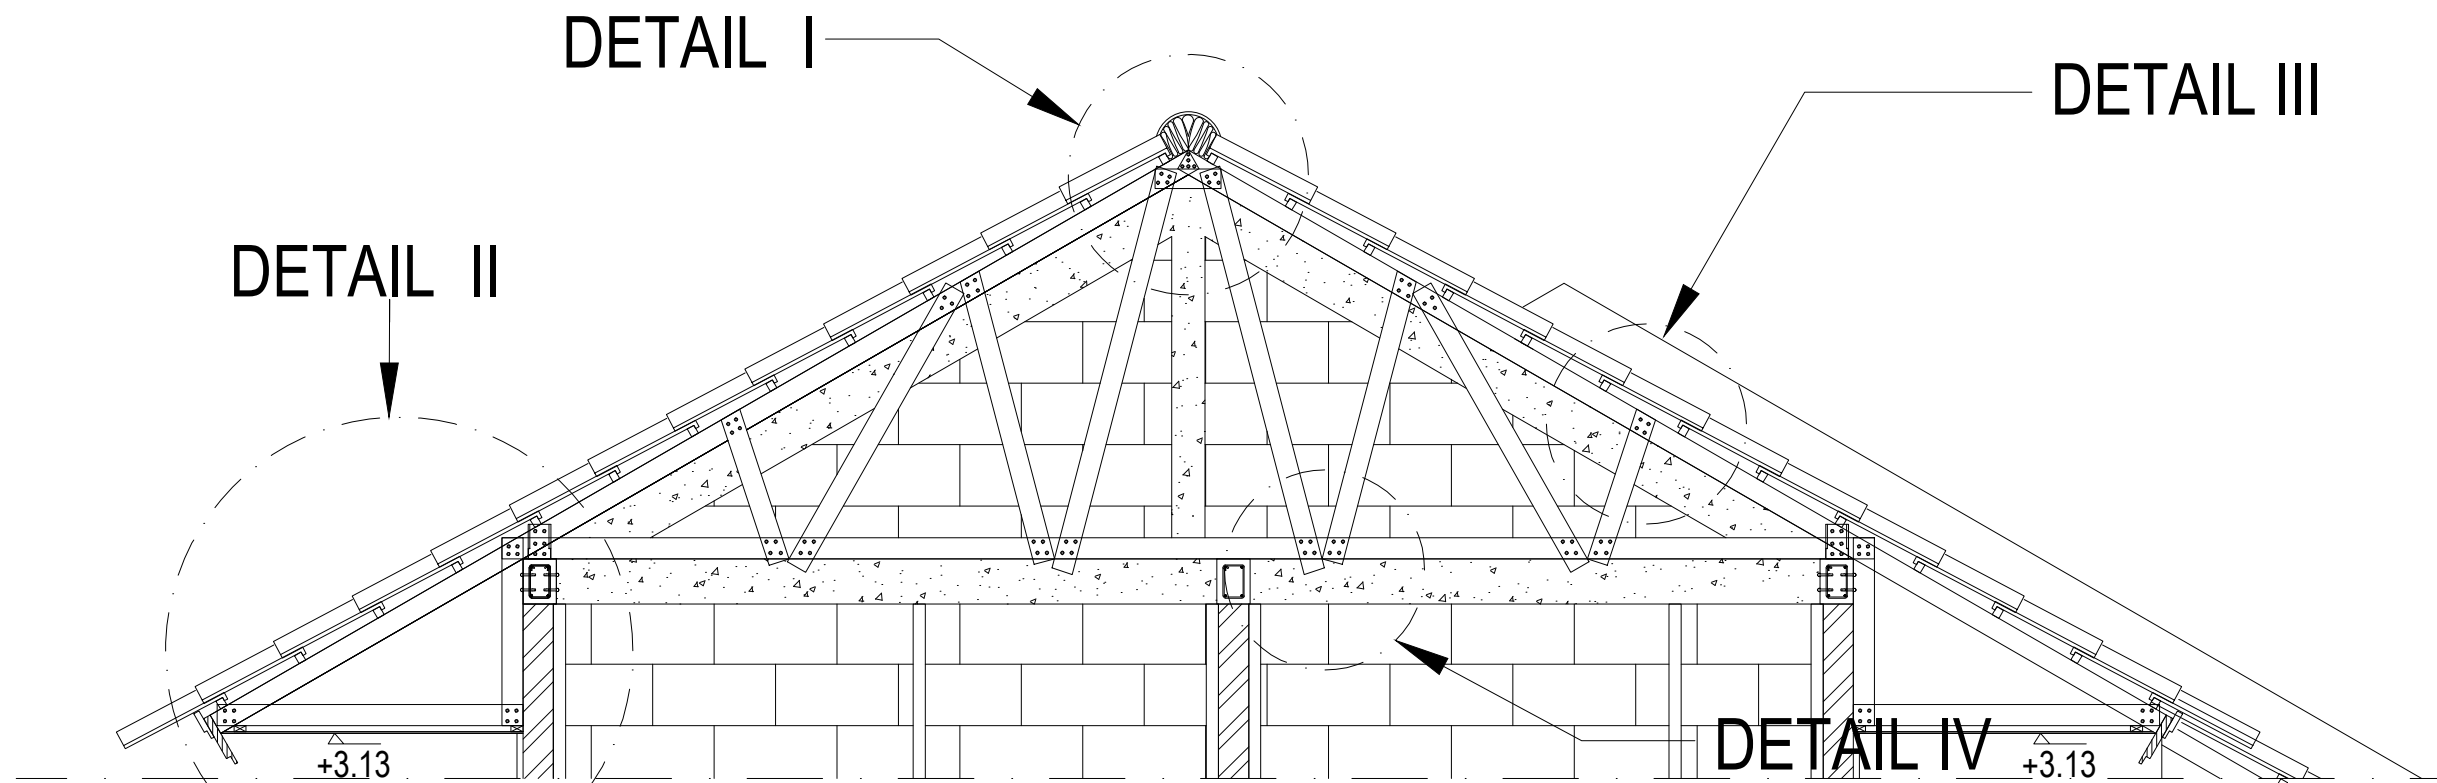


DETAIL KUDA-KUDA

Skala 1:20

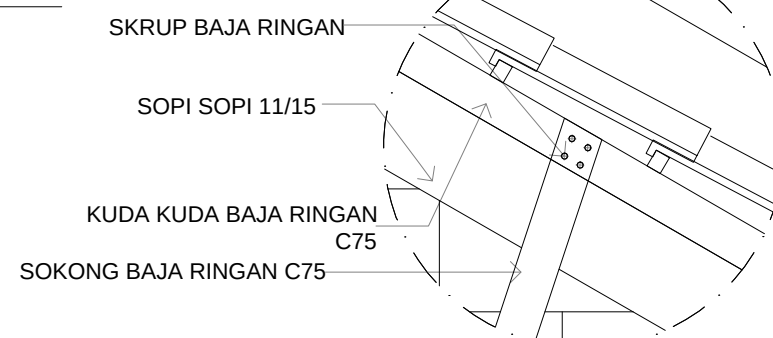


DETAIL III

Skala 1:10

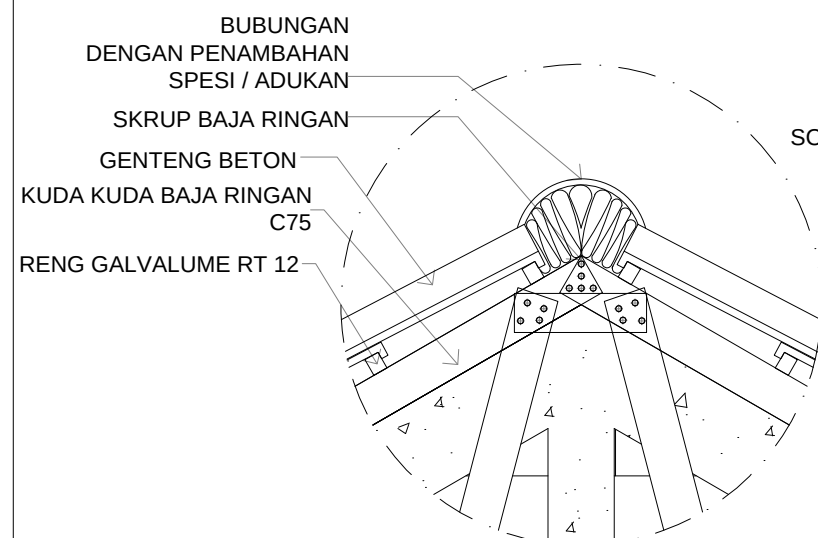


DETAIL I

Skala 1:10

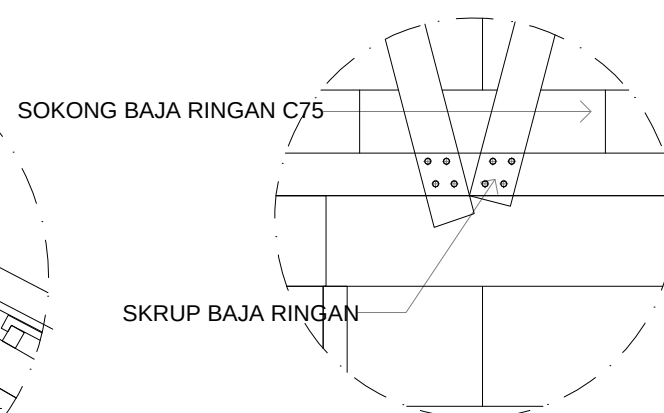

DETAIL IV

Skala 1:10

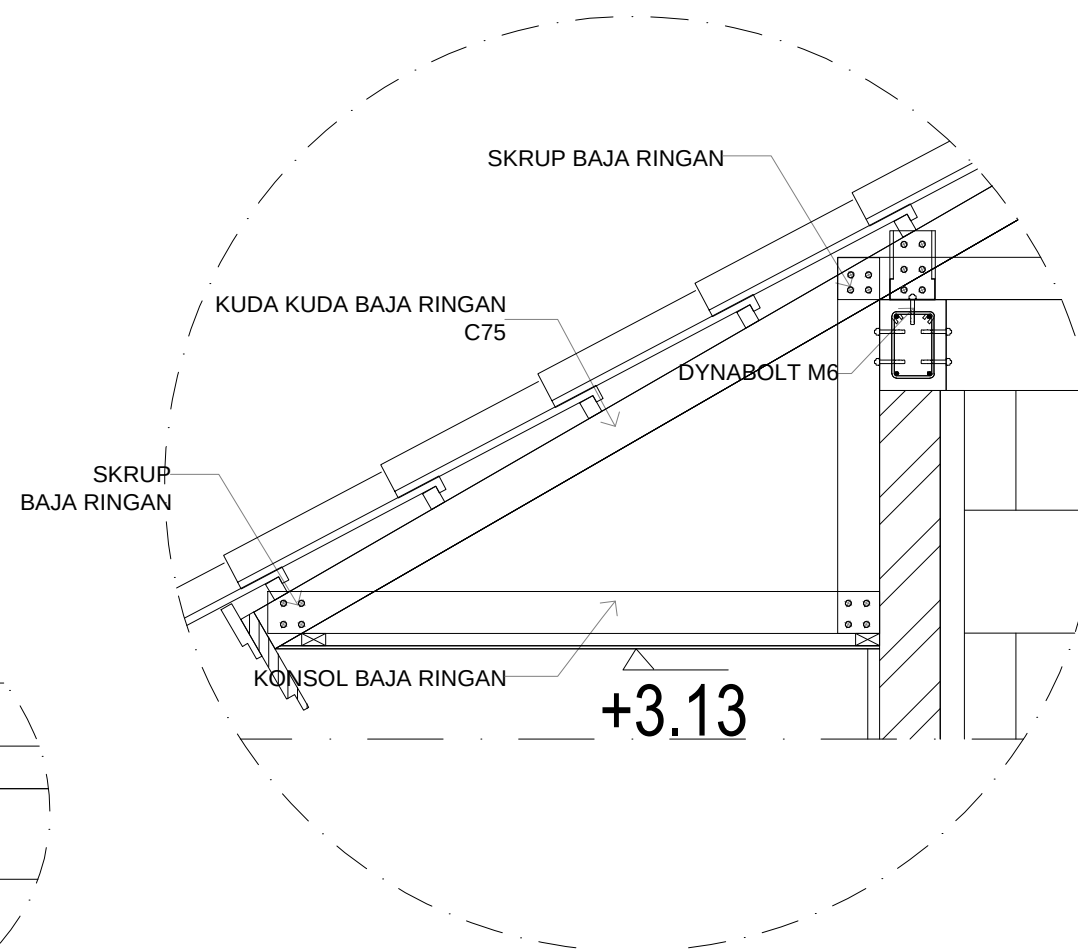


DETAIL II

Skala 1:10

CATATAN :

KETERANGAN

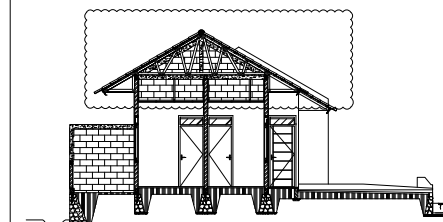

DEVELOPER



PT. KARYATARUNA ADHIPRATAMA
REAL ESTATE & DEVELOPER
Jalan Sukahaji No.126 Bandung 40152
Telp: (022) 82006365, 82006367 Fax: (022) 82006362

PROYEK

BUMI KARYA INDAH

GAMBAR

DETAIL KUDA KUDA

TYPE 25/72 (25.2)

SKALA 1:50

DIRENCANAKAN dan DIGAMBAR :

PURNAMA KUSUMA MAHBUB

DIPERIKSA:

RANI SHINTA HAPSARI

DISETUJUI :

AGNES STEPHANIA A. T.

NO. REVISI

TANGGAL

01.

NOMOR LEMBAR


JUMLAH LEMBAR

S-02-10


24

002_PL-BKI/EX/2572-2/ASDIR/VI/2022


20/06/2022

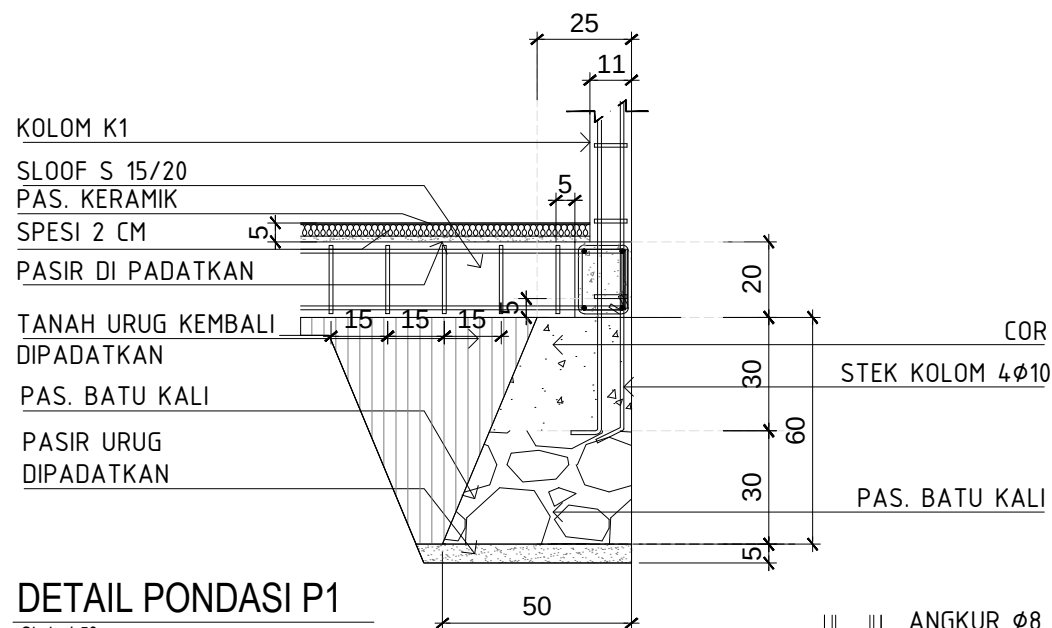


DETAIL PONDASI P1
Skala 1:50

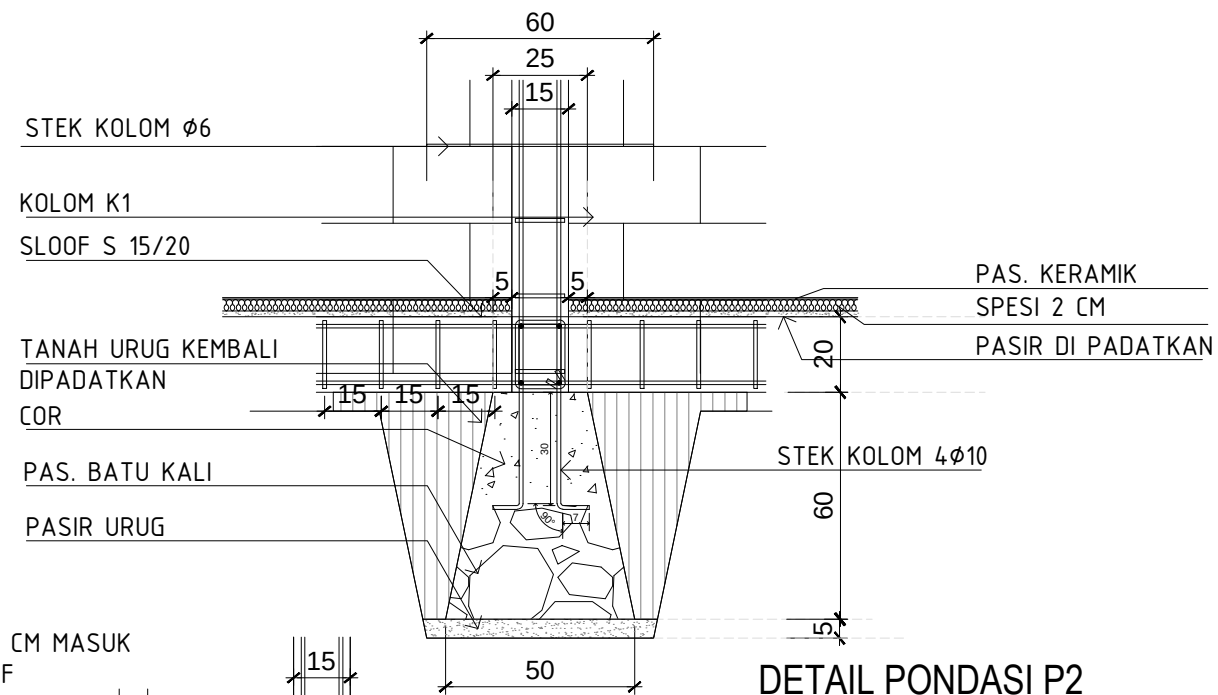


DETAIL PONDASI P2
Skala 1:50

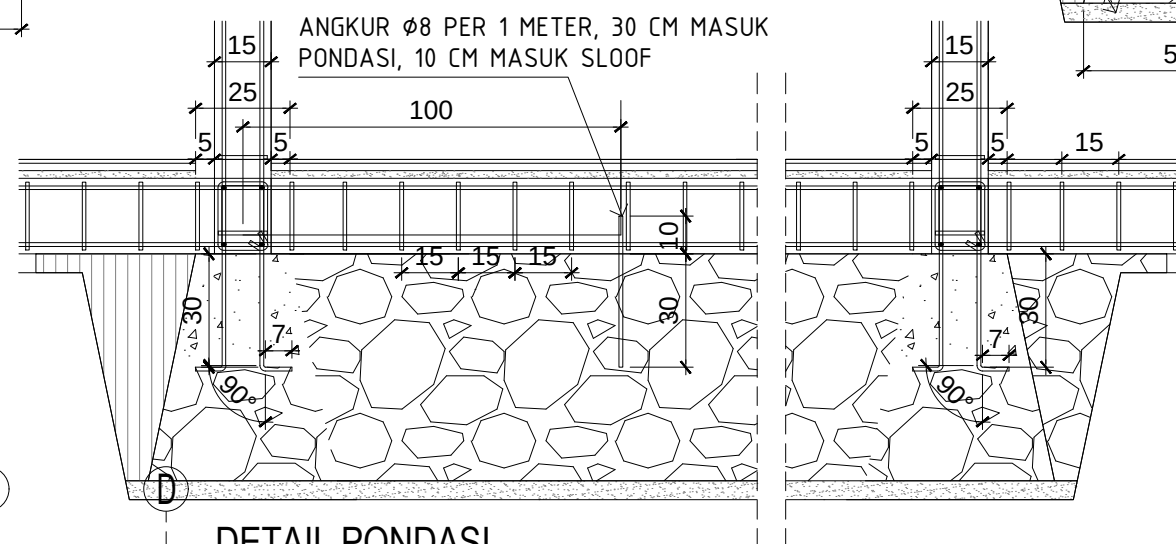

DETAIL PONDASI
Skala 1:50

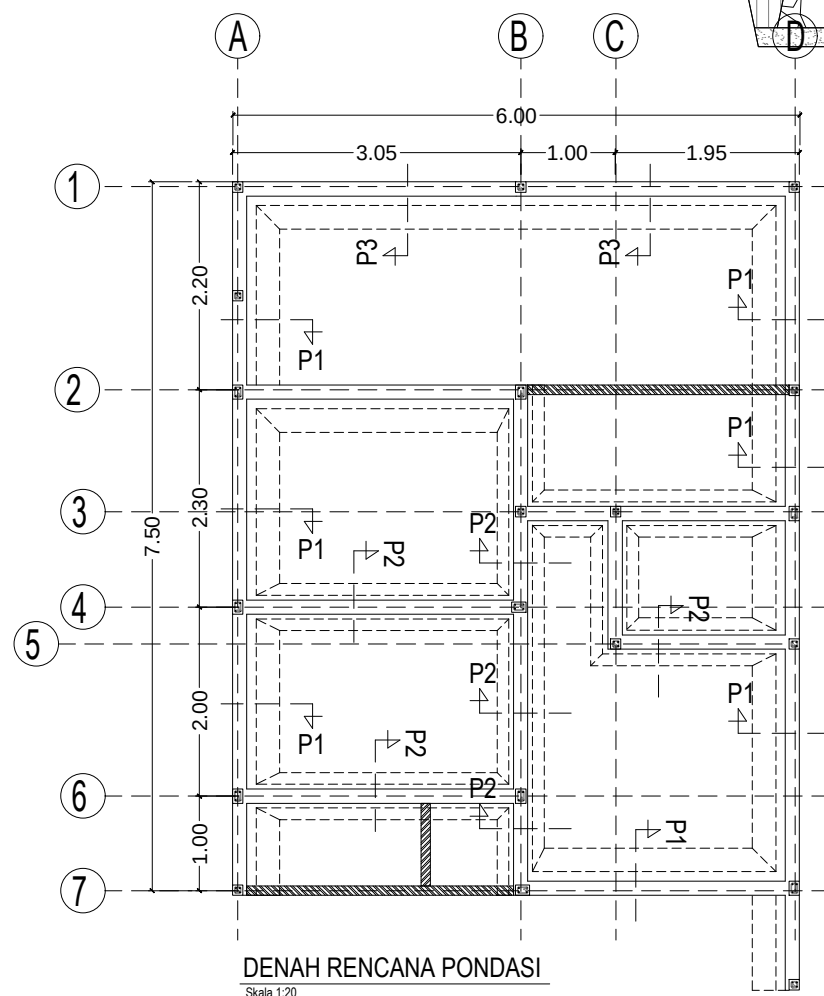

DENAH RENCANA PONDASI
Skala 1:20

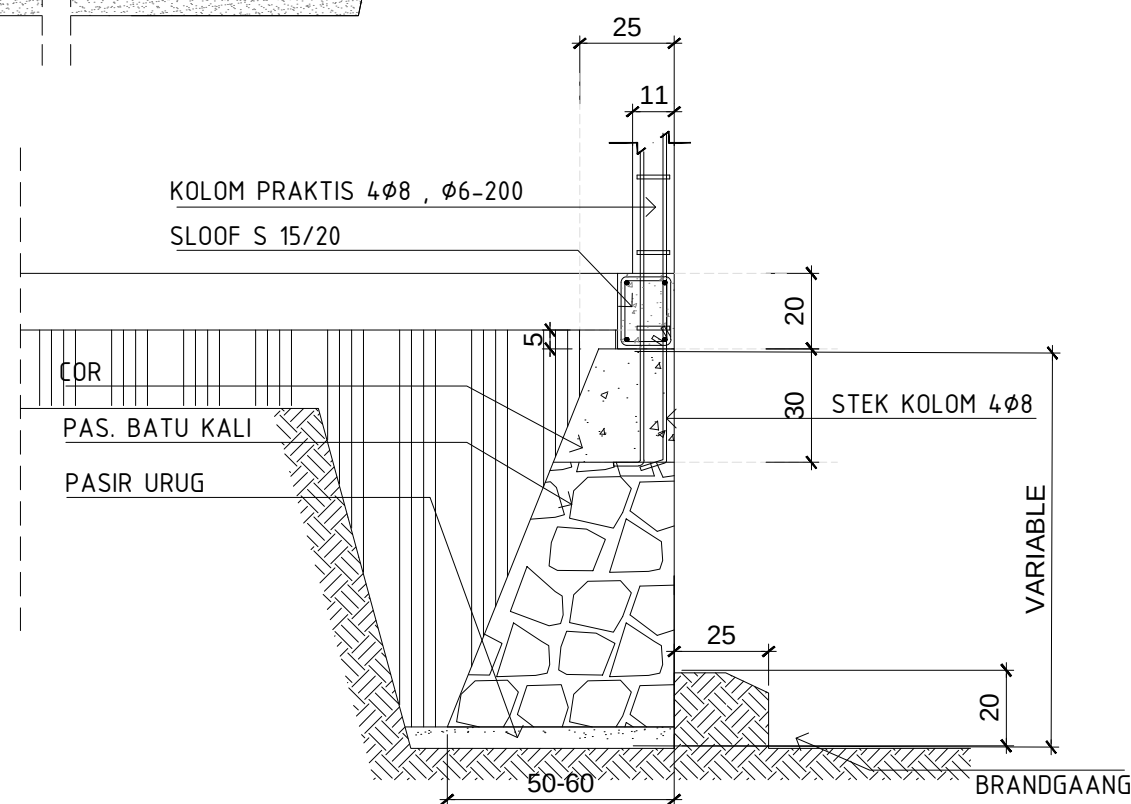

DETAIL PONDASI P3
Skala 1:50

CATATAN :

KETERANGAN

DEVELOPER



PT. KARYATARUNA ADHIPRATAMA
REAL ESTATE & DEVELOPER
Jalan Sukahaji No.126 Bandung 40152
Telp: (022) 82006365, 82006367 Fax: (022) 82006362

PROYEK

BUMI KARYA INDAH

GAMBAR

DETAIL PONDASI

TYPE 25/72 (25.2)

SKALA 1:20

DIRENCANAKAN dan DIGAMBAR :

PURNAMA KUSUMA MAHBUB

DIPERIKSA:

RANI SHINTA HAPSARI

DISETUJUI :

AGNES STEPHANIA A. T.

NO. REVISI

TANGGAL

01.

NOMOR LEMBAR

JUMLAH LEMBAR

S-03-11

24


002_PL-BKI/EX/2572-2/ASDIR/VI/2022

20/06/2022




DETAIL Plafond II

24

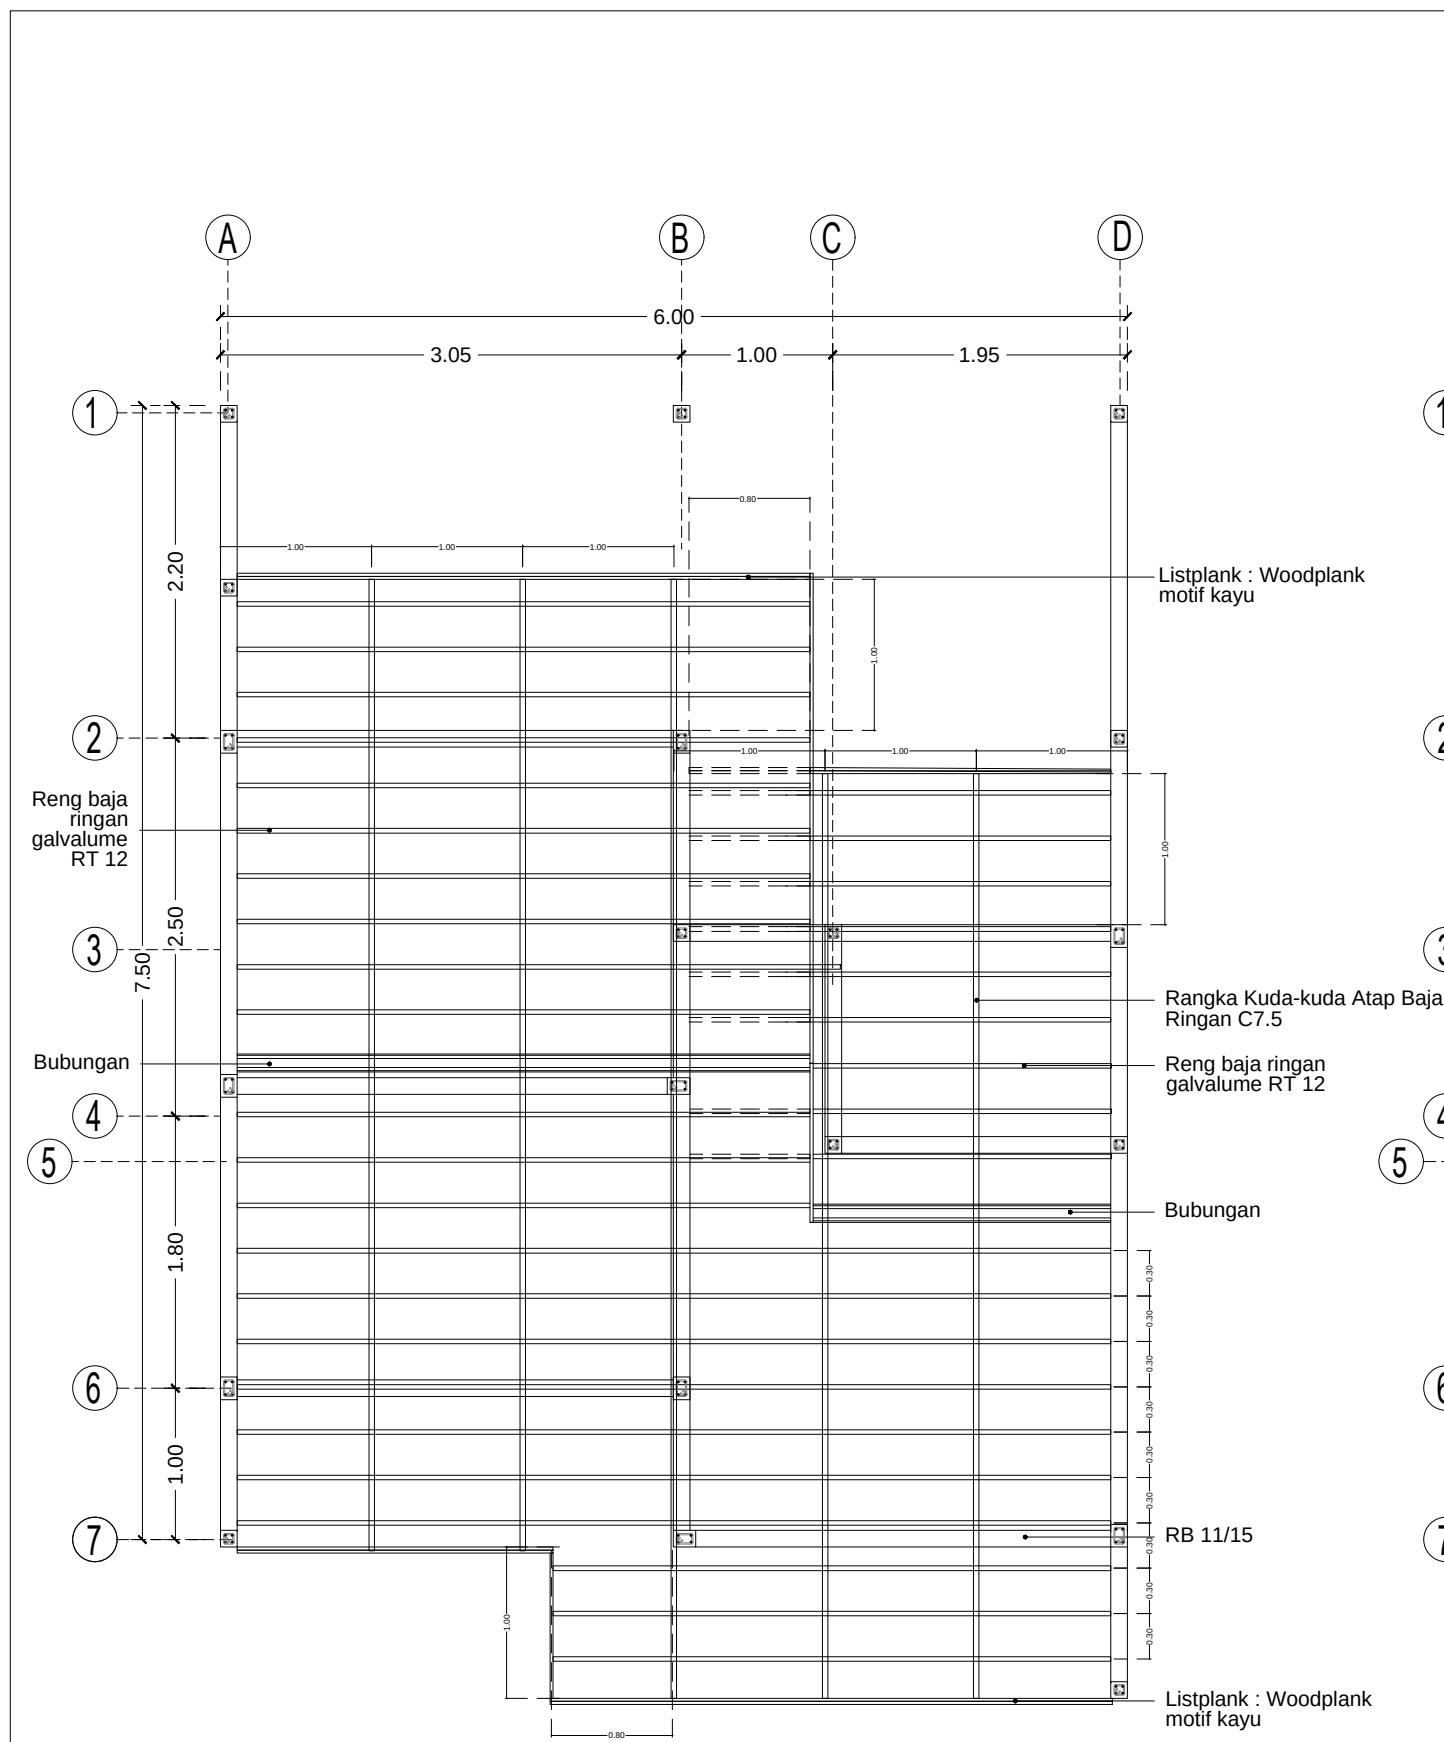

DENAH RENCANA ATAP

Skala 1:50

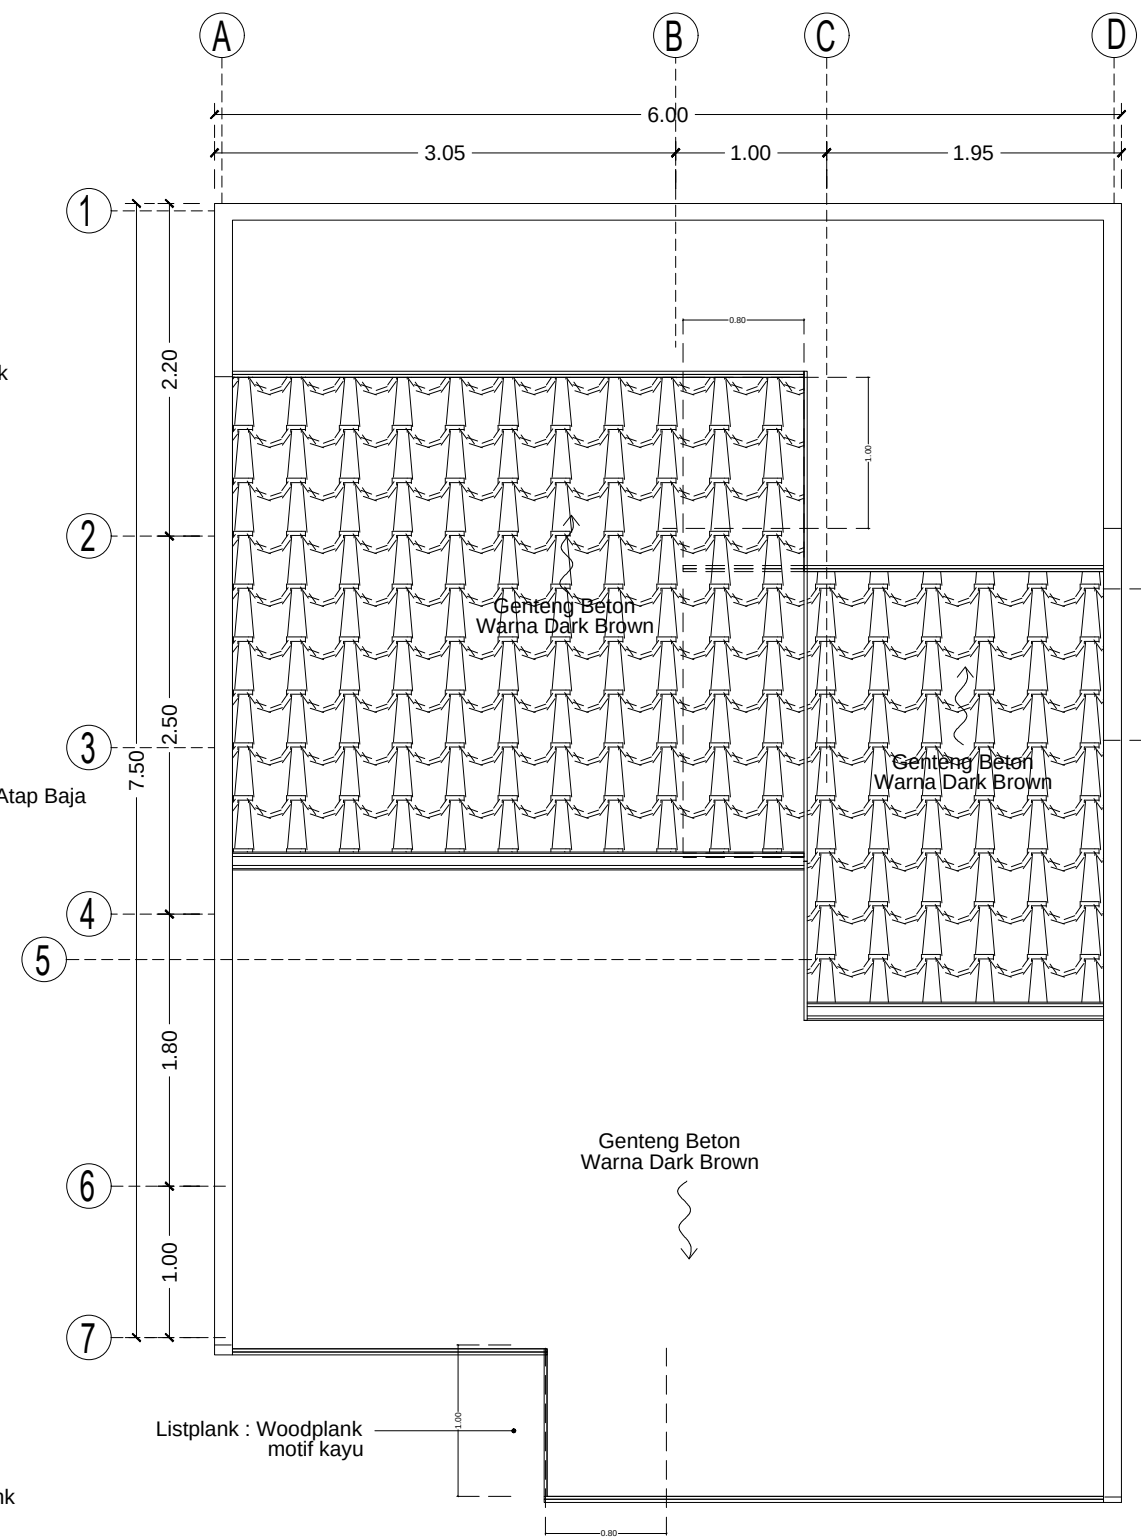


DENAH ATAP

Skala 1:50

CATATAN :

KETERANGAN

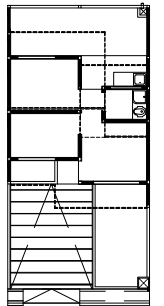

DEVELOPER



PT. KARYATARUNA ADHIPRATAMA
REAL ESTATE & DEVELOPER
Jalan Sukahaji No.126 Bandung 40152
Telp: (022) 82006365, 82006367 Fax: (022) 82006362

PROYEK

BUMI KARYA INDAH

GAMBAR

RENCANA ATAP

TYPE 25/72 (25.2)

SKALA 1:50

DIRENCANAKAN dan DIGAMBAR :

PURNAMA KUSUMA MAHBUB

DIPERIKSA:

RANI SHINTA HAPSARI

DISETUJUI :

AGNES STEPHANIA A. T.

NO. REVISI

TANGGAL

01.

NOMOR LEMBAR


JUMLAH LEMBAR

S-04-14

24

002_PL-BKI/EX/2572-2/ASDIR/VI/2022

20/06/2022




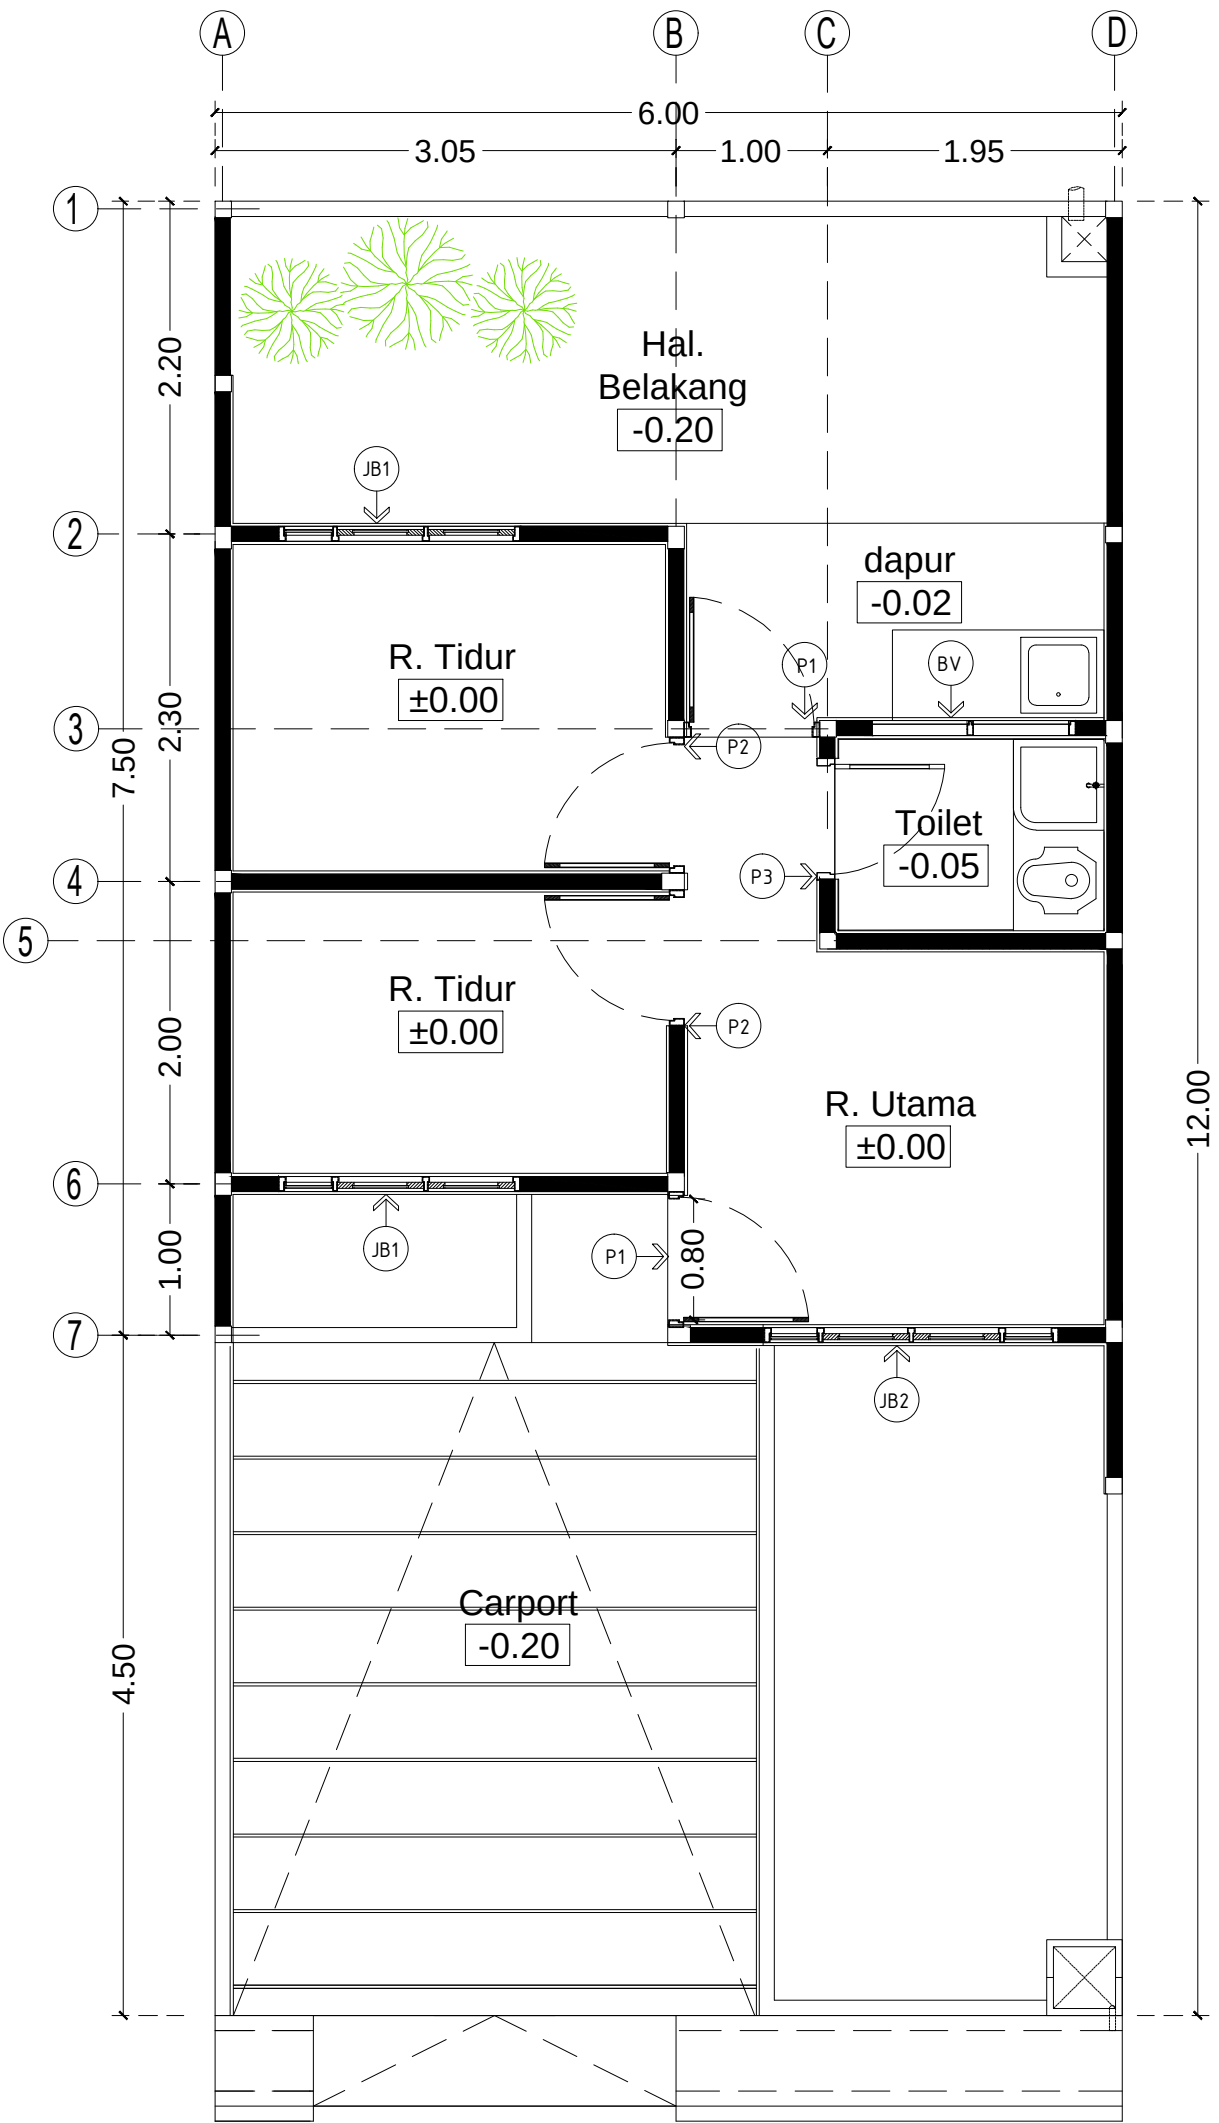





Denah Rencana Kusen



Skala 1:50


002_PL-BK/EX/2572-2/ASDIR/VI/2022 20/06/2022

CATATAN :	
KETERANGAN	
DEVELOPER	
 PT. KARYA ARUNA ADHIPRATAMA REAL ESTATE & DEVELOPER Jalan Sisinga No. 105 Bandung 40132 Telp. 022 52000000 02000000 Fax. 022 52000000	
PROYEK	
BUMI KARYA INDAH	
GAMBAR	
DENAH RENCANA KUSEN	
TYPE 25/72 (25.2)	
SKALA 1:50	
DIRENCANAKAN dan DIGAMBAR :	
PURNAMA KUSUMA MAHBUB	
DIPERIKSA:	
RANI SHINTA HAPSARI	
DISETUJUI :	
AGNES STEPHANIA A. T.	
NO. REVISI	
01.	TANGGAL
NOMOR LEMBAR	
A-07-15	JUMLAH LEMBAR
24	

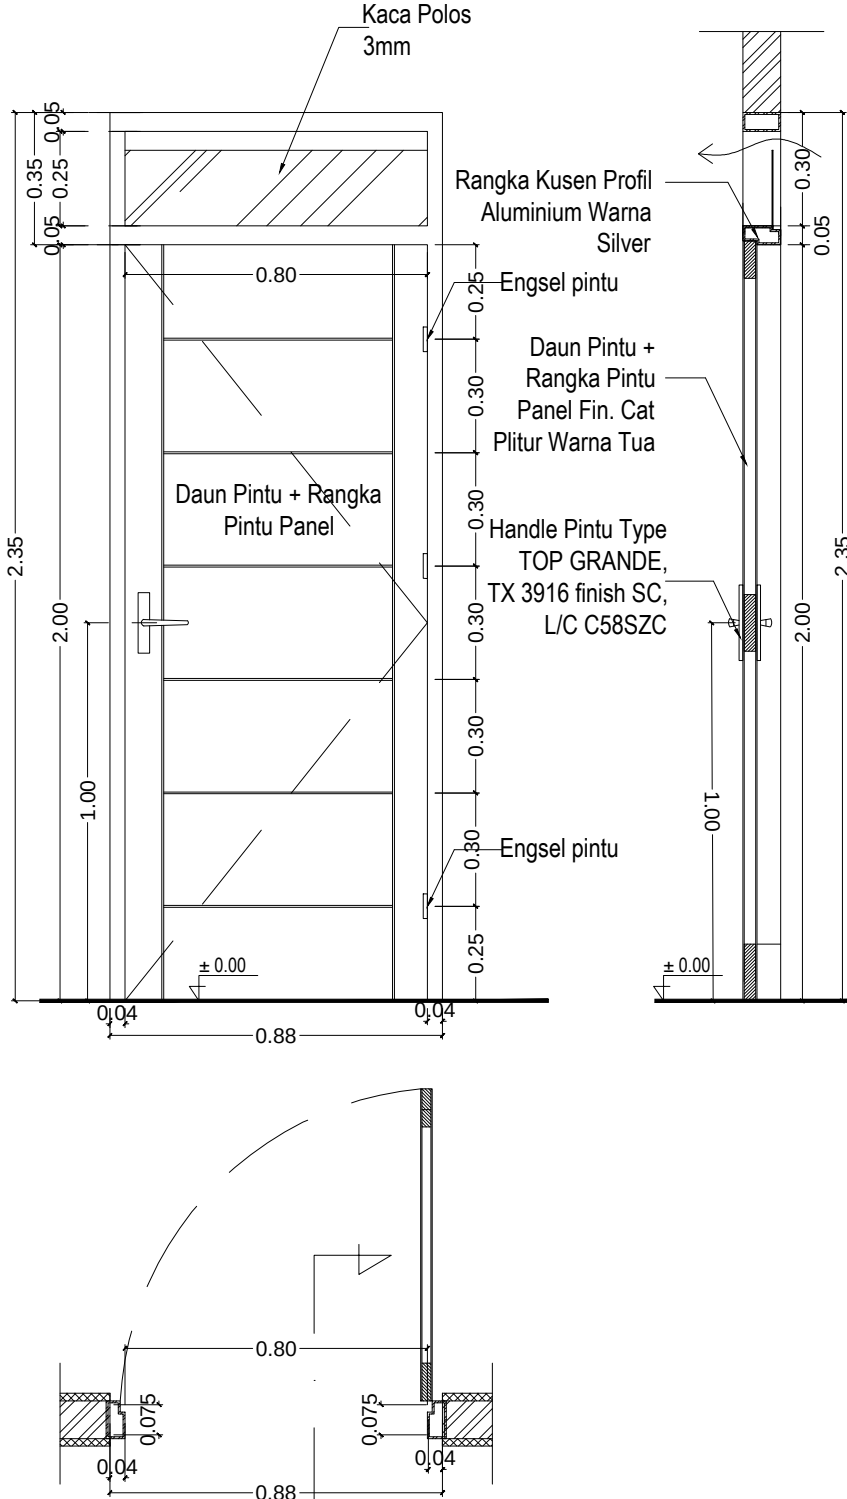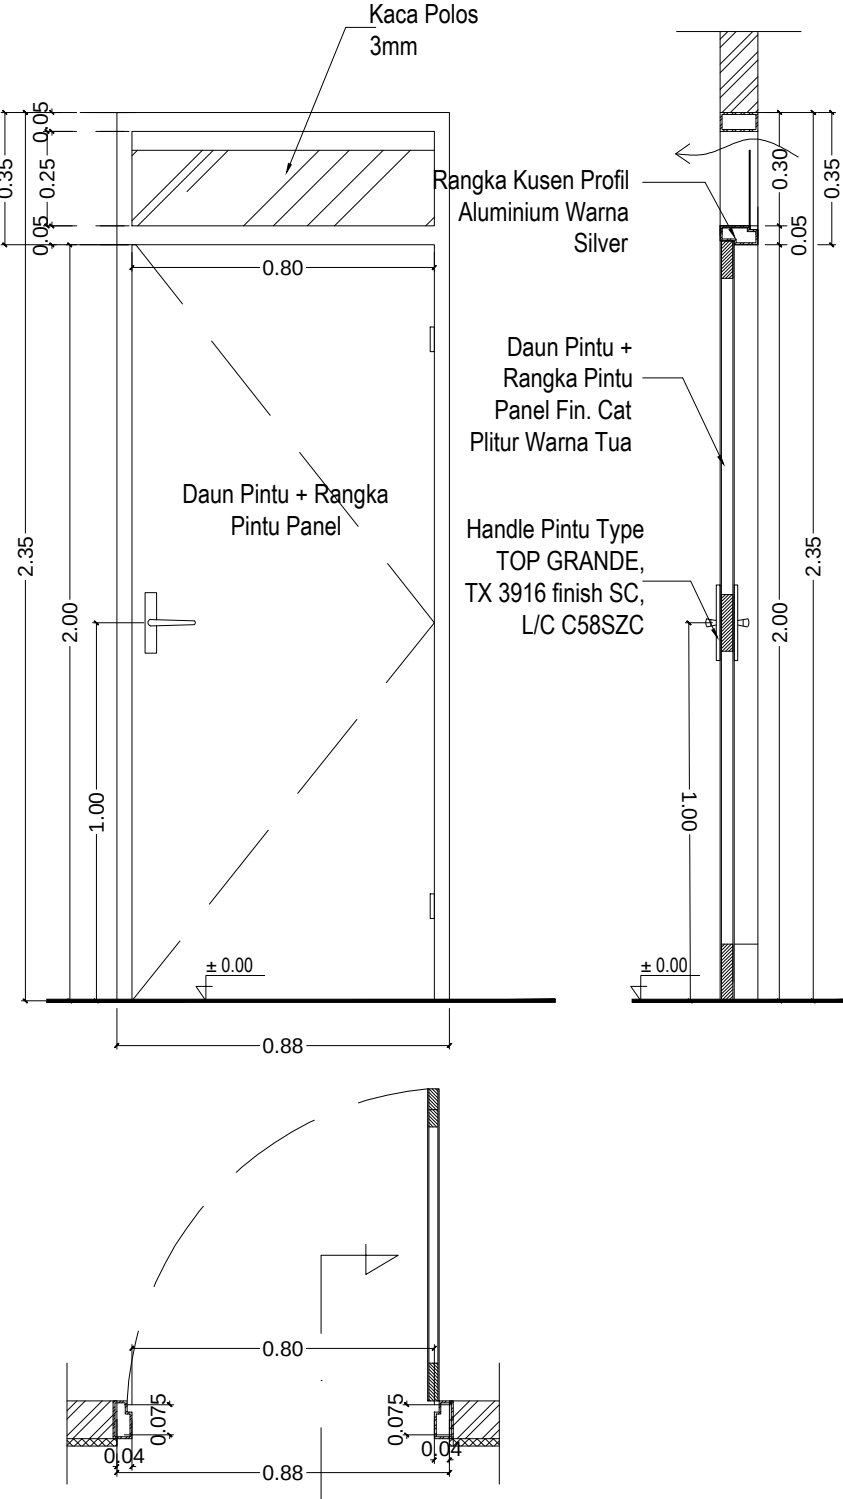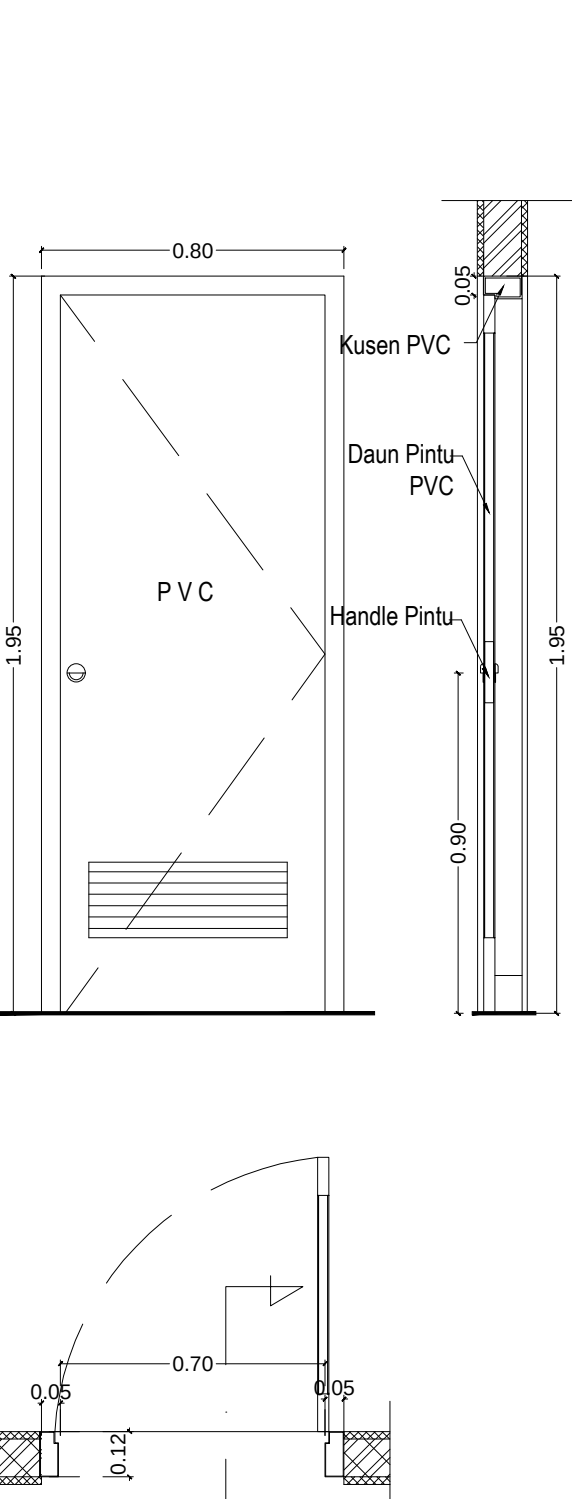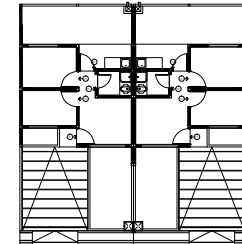TIPE	P1		P2		P3		CATATAN :	
GAMBAR							- Pintu depan dan belakang : 3 engsel - Pintu kamar : 2 engsel	
							KETERANGAN	
								
							DEVELOPER	
							 PT. KARYATARUNA ADHIPRATAMA REAL ESTATE & DEVELOPER Jln. Sukahaji 126 Bandung 40152 Telp: (022) 82006365, 82006367 Fax: (022) 82006362	
						PROYEK		
						BUMI KARYA INDAH		
						GAMBAR		
						DETAIL KUSEN		
						TYPE 25/72 (25.2)1:20		
						DIRENCANAKAN dan DIGAMBAR :		
						PURNAMA KUSUMA MAHBUB		
						DIPERIKSA:		
						RANI SHINTA HAPSARI		
						DISETUJUI :		
						AGNES STEPHANIA A. T.		
						NO. REVISI		
						TANGGAL		
						NOMOR LEMBAR		
						JUMLAH LEMBAR		
				002_PL-BKI/EX/2572-2/ASDIR/VI/2022		20/06/2022		
						A-08-16		
						24		

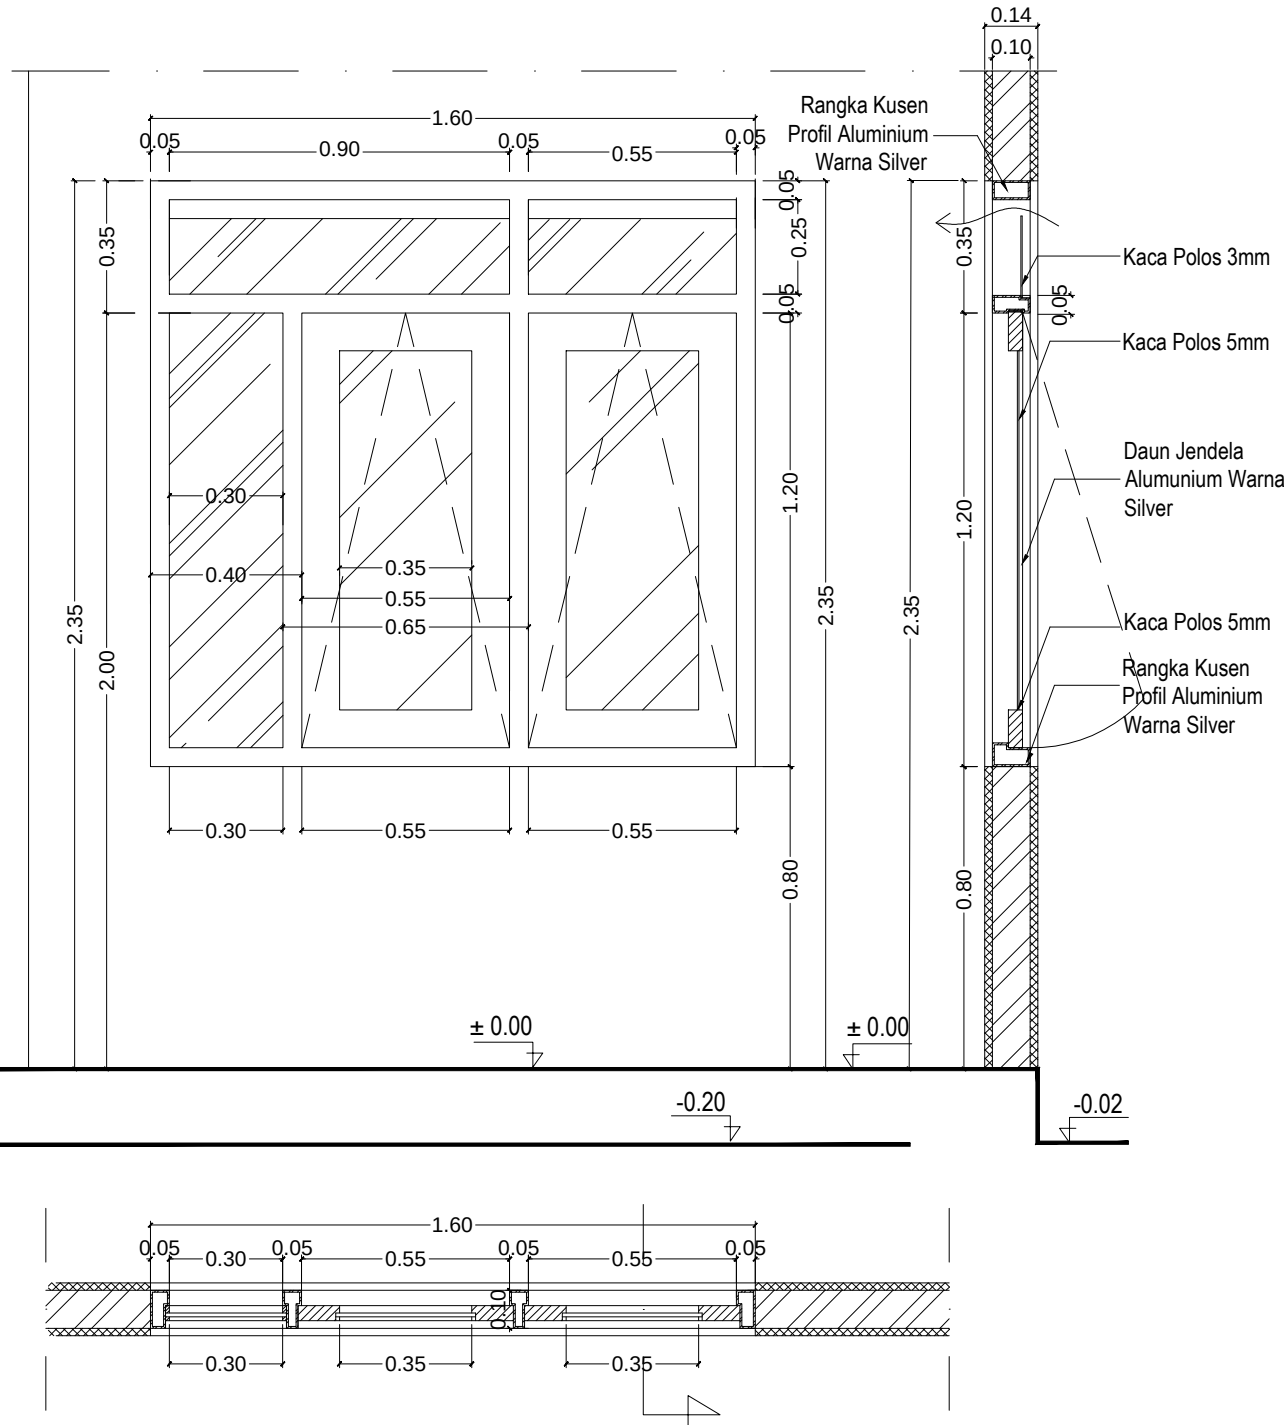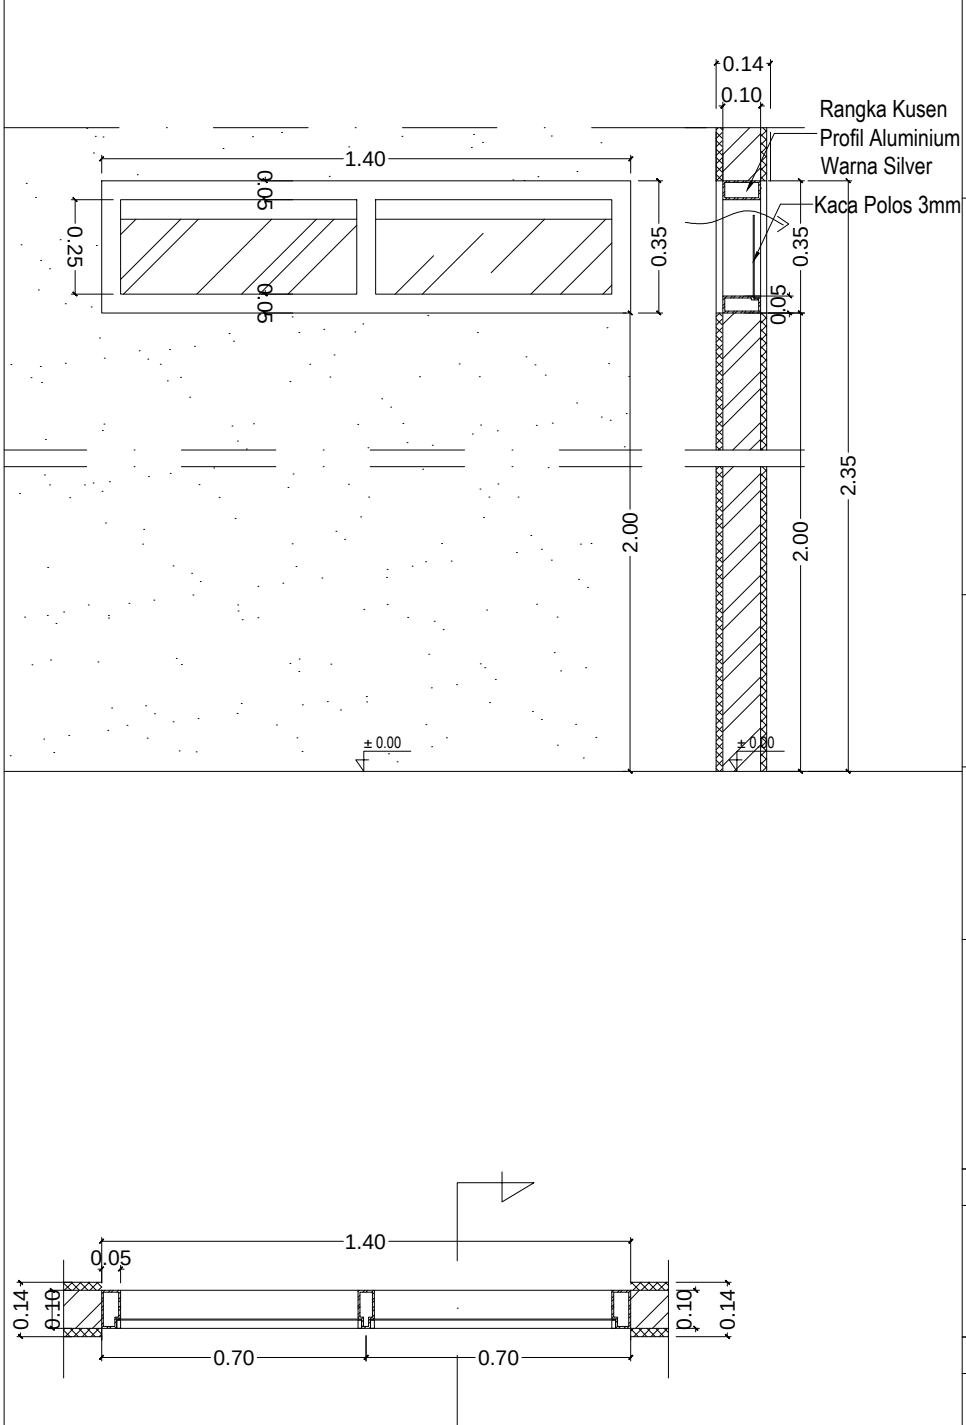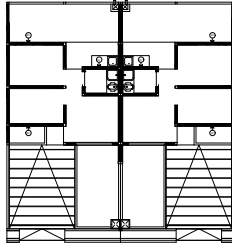
TIPE	JB1		BV		CATATAN :
GAMBAR					CATATAN :
					KETERANGAN
					
					DEVELOPER  PT. KARYATARUNA ADHIPRATAMA REAL ESTATE & DEVELOPER Jln. Sukahaji 126 Bandung 40152 Telp: (022) 82006365, 82006367 Fax: (022) 82006362
					PROYEK BUMI KARYA INDAH
MATERIAL					GAMBAR DETAIL KUSEN
					TYPE 25/72 (25.2) 1:20
					DIRENCANAKAN dan DIGAMBAR :
					PURNAMA KUSUMA MAHBUB
					DIPERIKSA:
JUMLAH					RANI SHINTA HAPSARI
					DISETUJUI : AGNES STEPHANIA A. T.
					NO. REVISI TANGGAL
					NOMOR LEMBAR JUMLAH LEMBAR
					A-09-17 24
			002_PL-BKI/EX/2572-2/ASDIR/VI/2022		20/06/2022

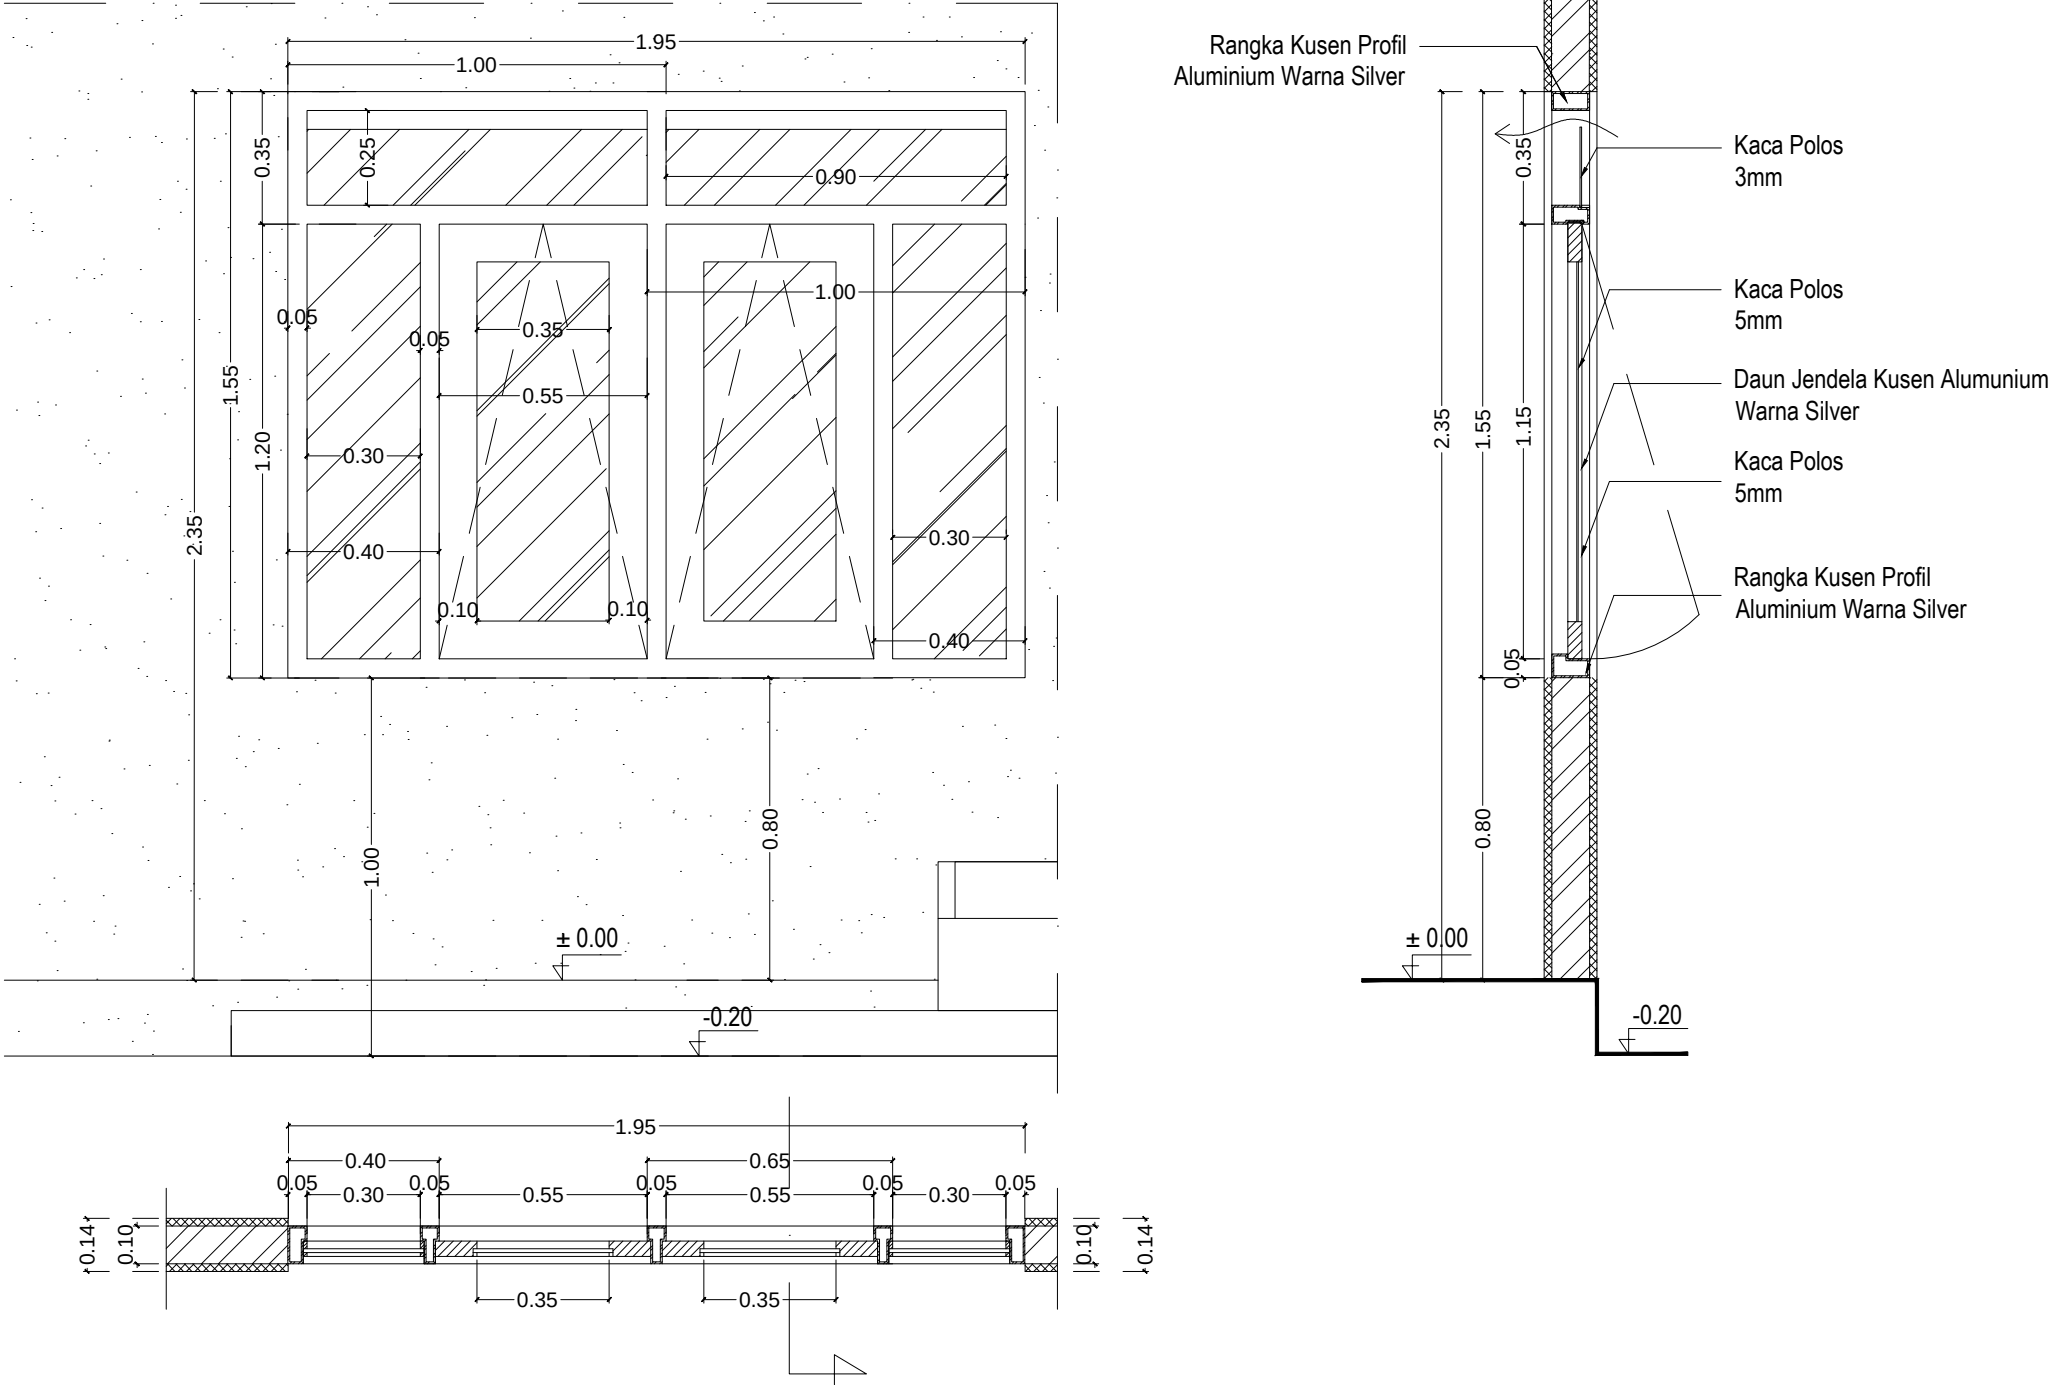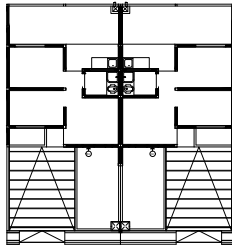TIPE	JB2		CATATAN :	
GAMBAR				
			KETERANGAN 	
			DEVELOPER  PT. KARYATARUNA ADHIPRATAMA REAL ESTATE & DEVELOPER Jln. Sukahaji 126 Bandung 40152 Telp: (022) 82006365, 82006367 Fax: (022) 82006362	
			PROYEK BUMI KARYA INDAH	
			GAMBAR DETAIL KUSEN TYPE 25/72 (25.2) 1:20 DIRENCANAKAN dan DIGAMBAR :	
MATERIAL	KUSEN	Rangka Kusen Profil Aluminium Ex. Alco Warna Silver	RANI SHINTA HAPSARI	
	DAUN PINTU	-	DIPERIKSA:	
	DAUN JENDELA	Kusen Alumunium Warna Silver	AGNES STEPHANIA A. T.	
JUMLAH	LANTAI 1	1 Unit	NO. REVISI	TANGGAL
	LOKASI	Teras Depan	NOMOR LEMBAR	JUMLAH LEMBAR
			002_PL-BKI/EX/2572-2/ASDIR/VI/2022	20/06/2022
			A-10-18	24

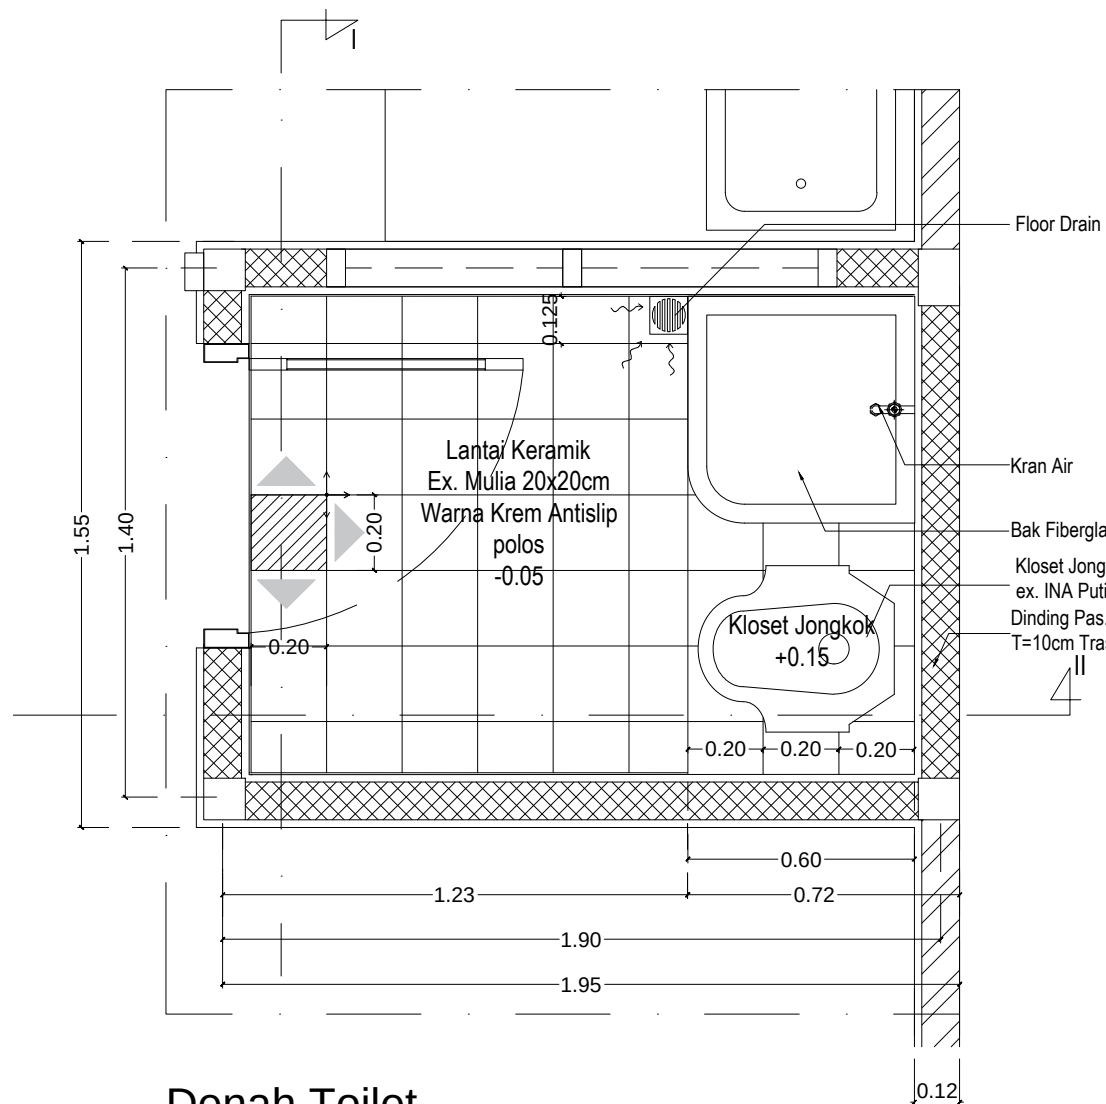


Denah Toilet

Skala 1 : 20

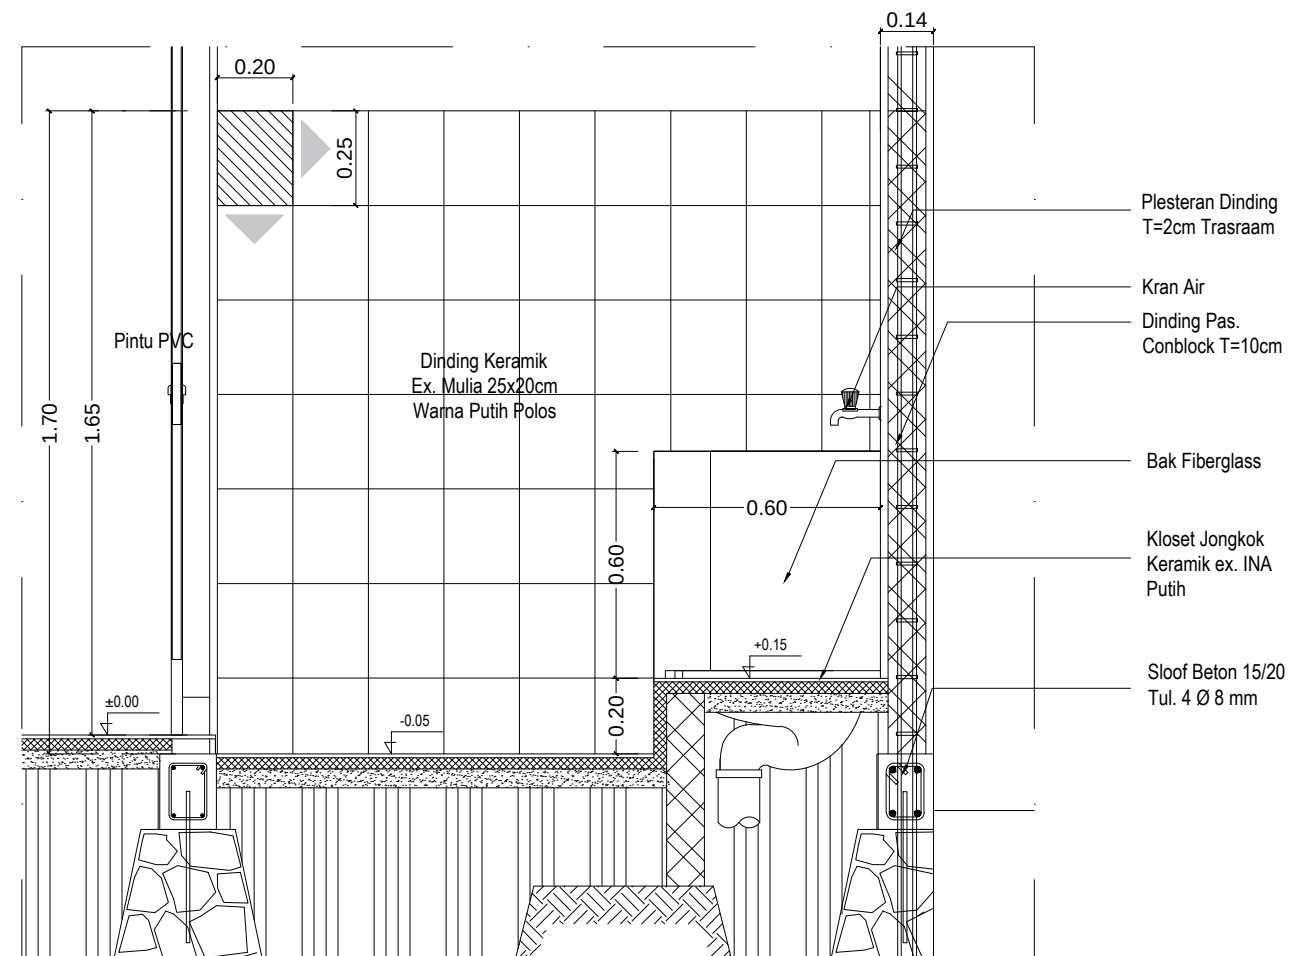

DETAIL Toilet II

Skala 1 : 20

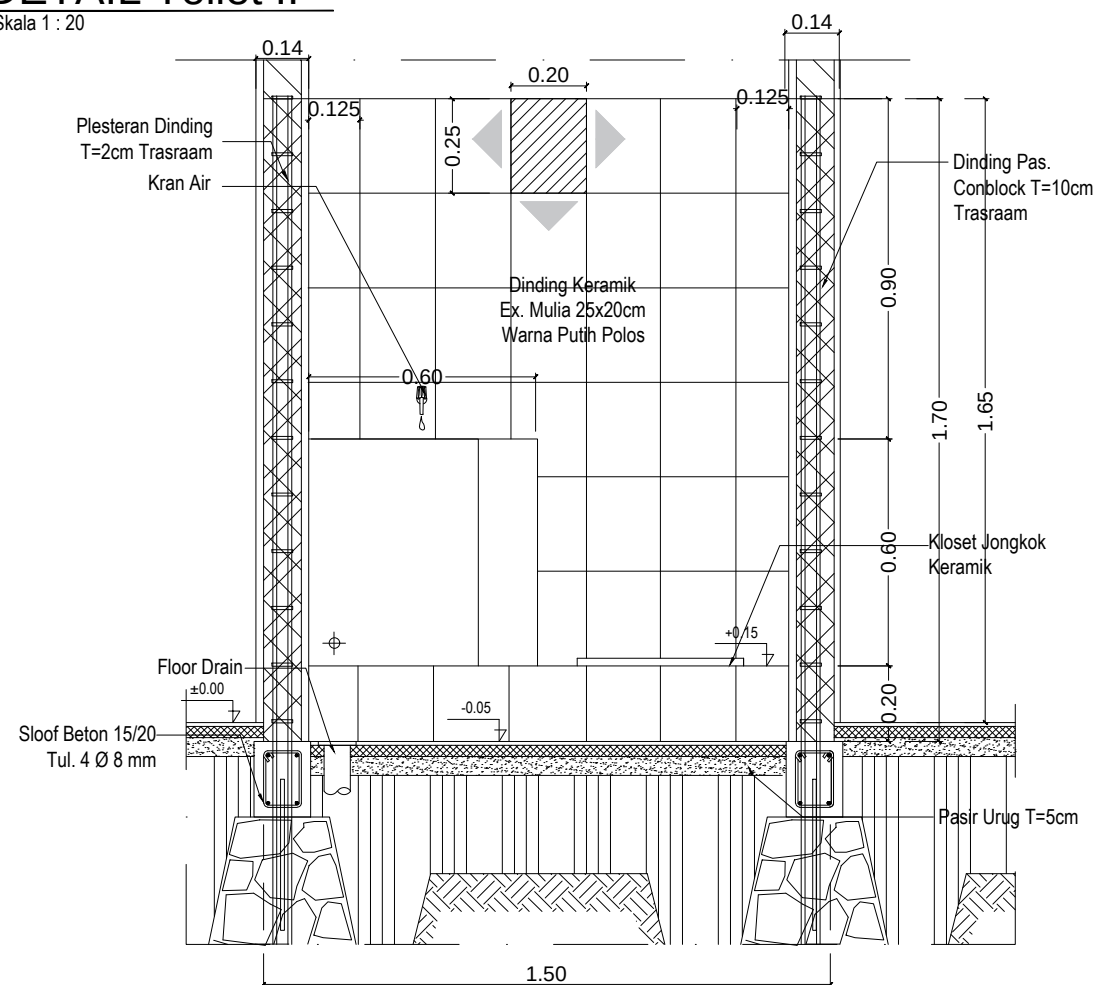


DETAIL Toilet I

Skala 1 : 20

CATATAN :



KETERANGAN

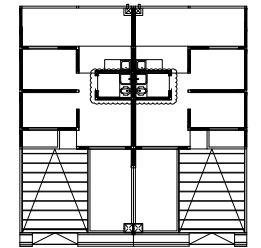

DEVELOPER



PT. KARYATARUNA ADHIPRATAMA
REAL ESTATE & DEVELOPER
Jln. Sukahaji 126 Bandung 40152
Telp: (022) 82006365, 82006367 Fax: (022) 82006362

PROYEK

BUMI KARYA INDAH

GAMBAR

DETAIL TOILET

TYPE 25/72 (25.2)

1:20

DIRENCANAKAN dan DIGAMBAR :

PURNAMA KUSUMA MAHBUB

DIPERIKSA:

RANI SHINTA HAPSARI

DISETUJUI :

AGNES STEPHANIA A. T.

NO. REVISI

TANGGAL

NOMOR LEMBAR


JUMLAH LEMBAR

S-05-19

24


002_PL-BKI/EX/2572-2/ASDIR/VI/2022

20/06/2022

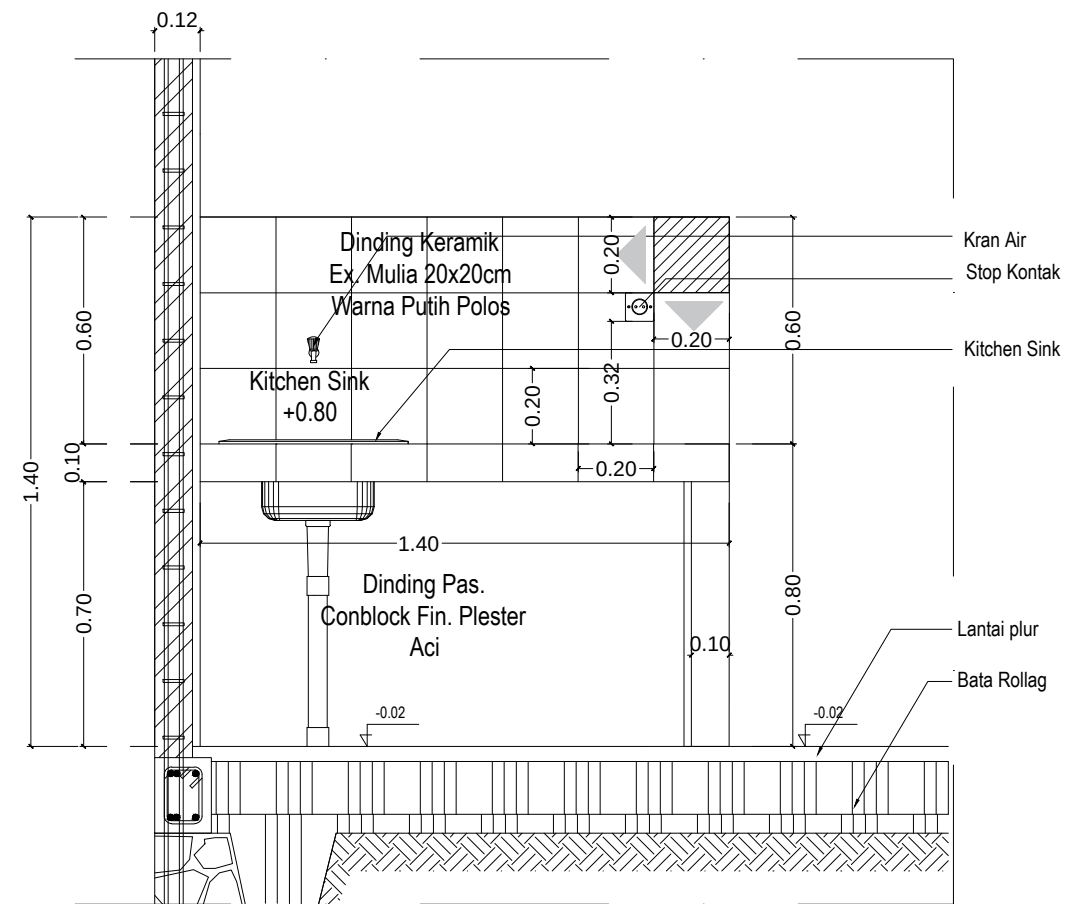


DETAIL Dapur I

Skala 1 : 20

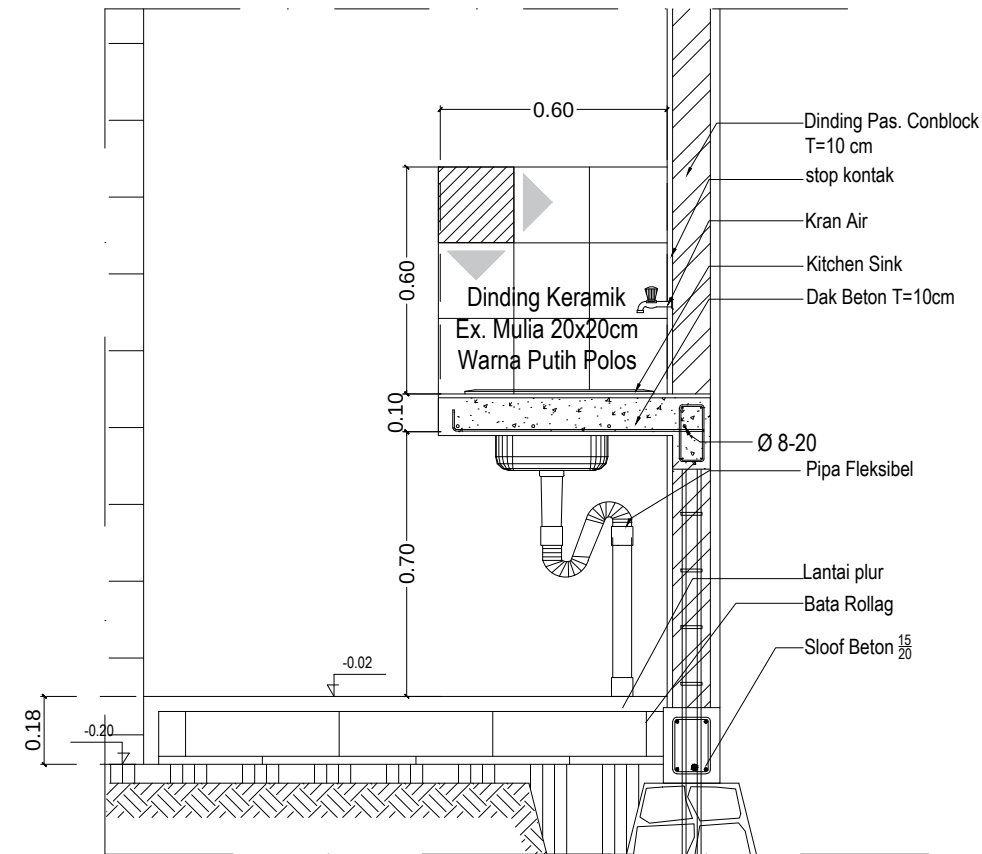

DETAIL Dapur II

Skala 1 : 20

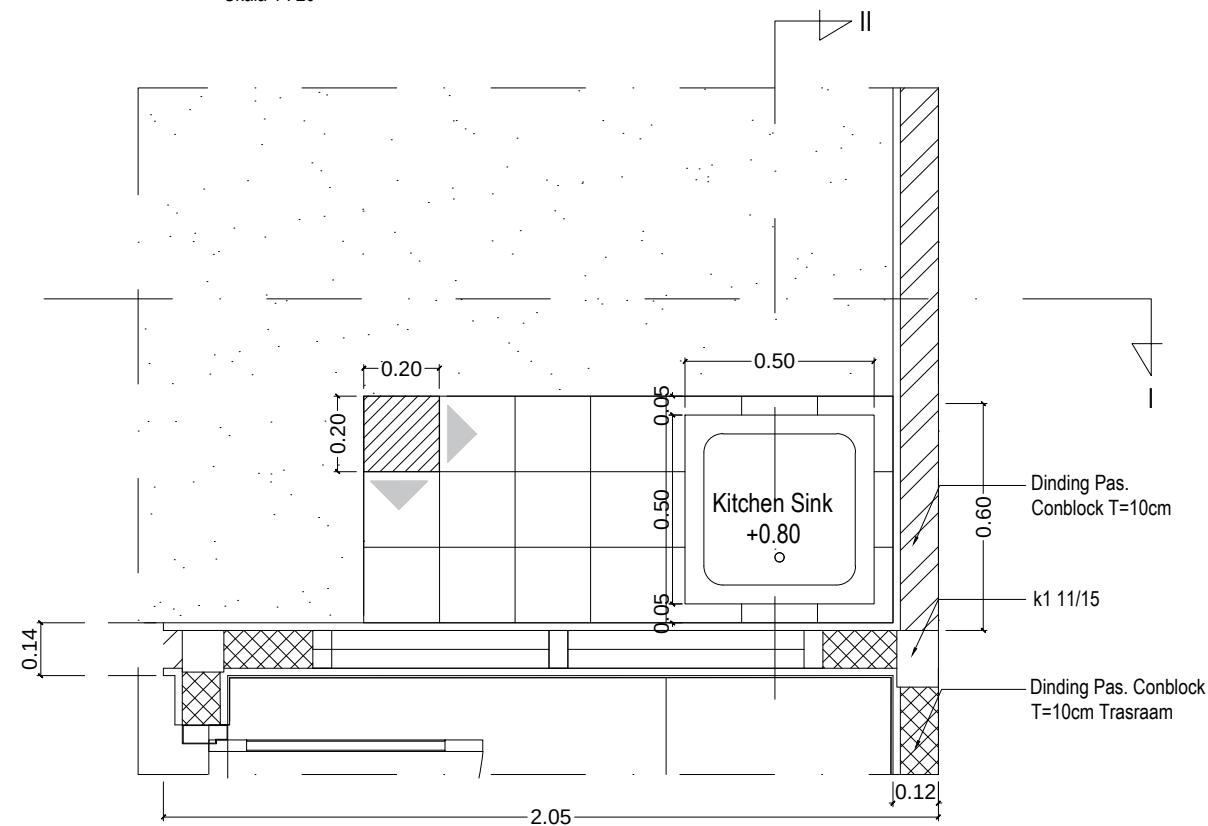


Denah Dapur

Skala 1 : 20

CATATAN :

KETERANGAN

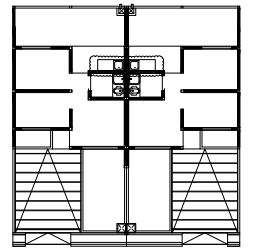

DEVELOPER



PT. KARYATARUNA ADHIPRATAMA
REAL ESTATE & DEVELOPER
 Jln. Sukahaji 126 Bandung 40152
 Telp: (022) 82006365, 82006367 Fax: (022) 82006362

PROYEK

BUMI KARYA INDAH

GAMBAR

DETAIL MEJA DAPUR

TYPE 25/72 (25.2)

1:20

DIRENCANAKAN dan DIGAMBAR :

PURNAMA KUSUMA MAHBUB

DIPERIKSA:

RANI SHINTA HAPSARI

DISETUJUI :

AGNES STEPHANIA A. T.

NO. REVISI

TANGGAL

NOMOR LEMBAR


Jumlah Lembar

S-06-20


24

002_PL-BKI/EX/2572-2/ASDIR/VI/2022


20/06/2022

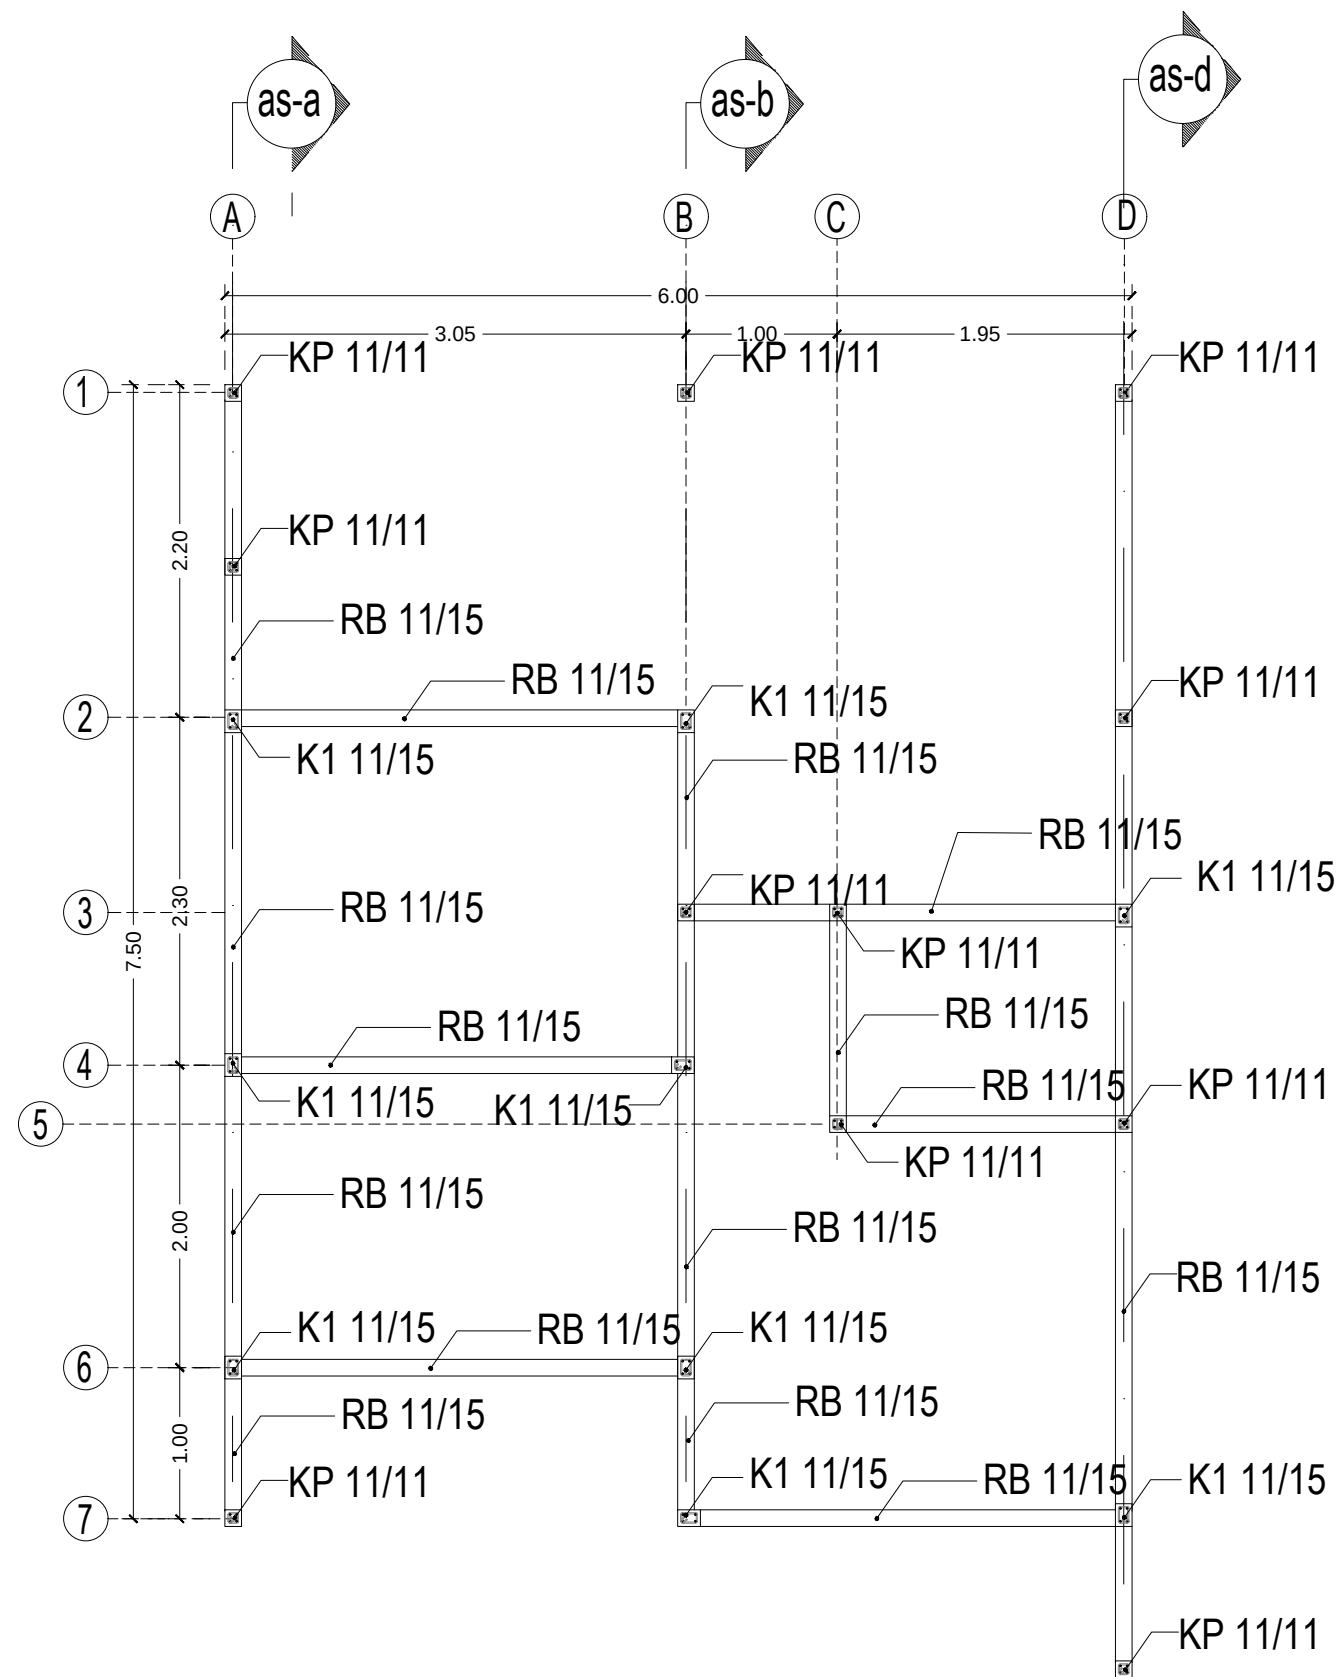


DENAH RENCANA PORTAL
Skala 1:50

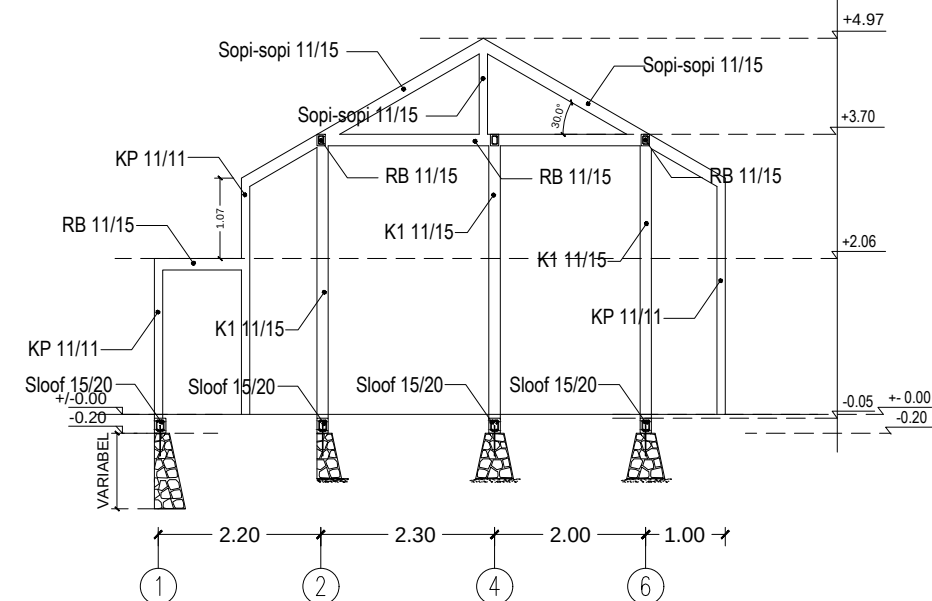

PORTAL As A
Skala 1 : 100

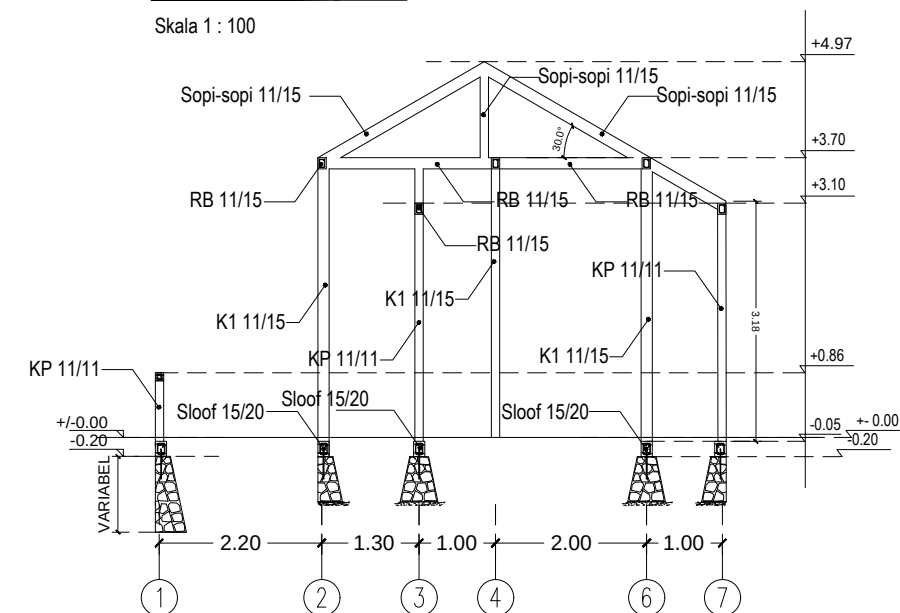


PORTAL As B
Skala 1 : 100

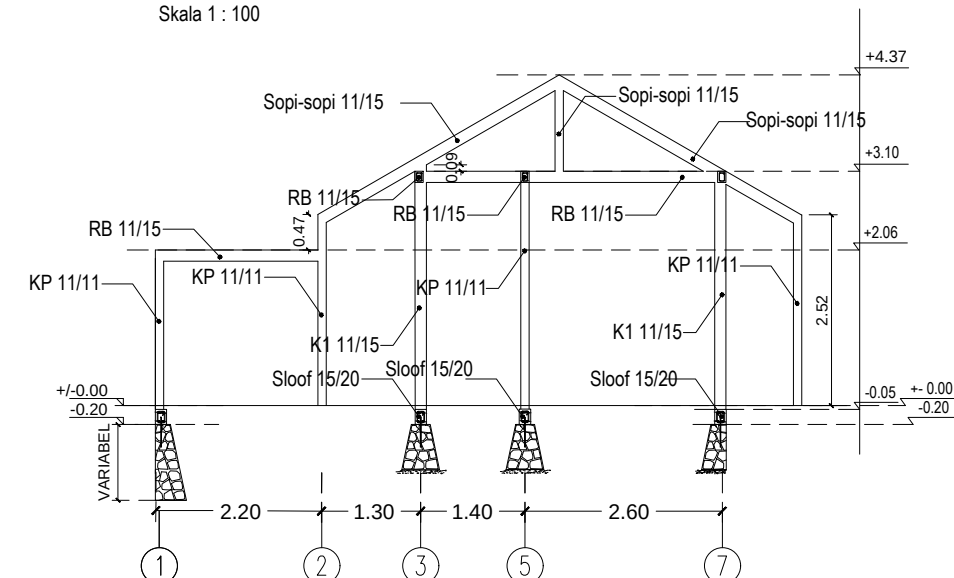

PORTAL As D
Skala 1 : 100

CATATAN :

KETERANGAN

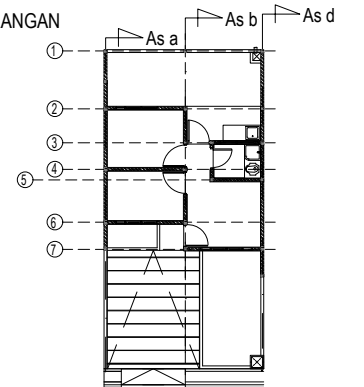

DEVELOPER



PT. KARYATARUNA ADHIPRATAMA
REAL ESTATE & DEVELOPER
Jalan Sukahaji No.126 Bandung 40152
Telp. (022) 82006365, 82006367 Fax: (022) 82006362

PROYEK

BUMI KARYA INDAH

GAMBAR

SKEMA STRUKTUR

TYPE 25/72 (25.2)

SKALA 1:50

DIRENCANAKAN dan DIGAMBAR :

PURNAMA KUSUMA MAHBUB

DIPERIKSA:

RANI SHINTA HAPSARI

DISETUJUI :

AGNES STEPHANIA A. T.

NO. REVISI

TANGGAL

01.

NOMOR LEMBAR


JUMLAH LEMBAR

S-07-21







24

002_PL-BKI/EX/2572-2/ASDIR/VI/2022


20/06/2022

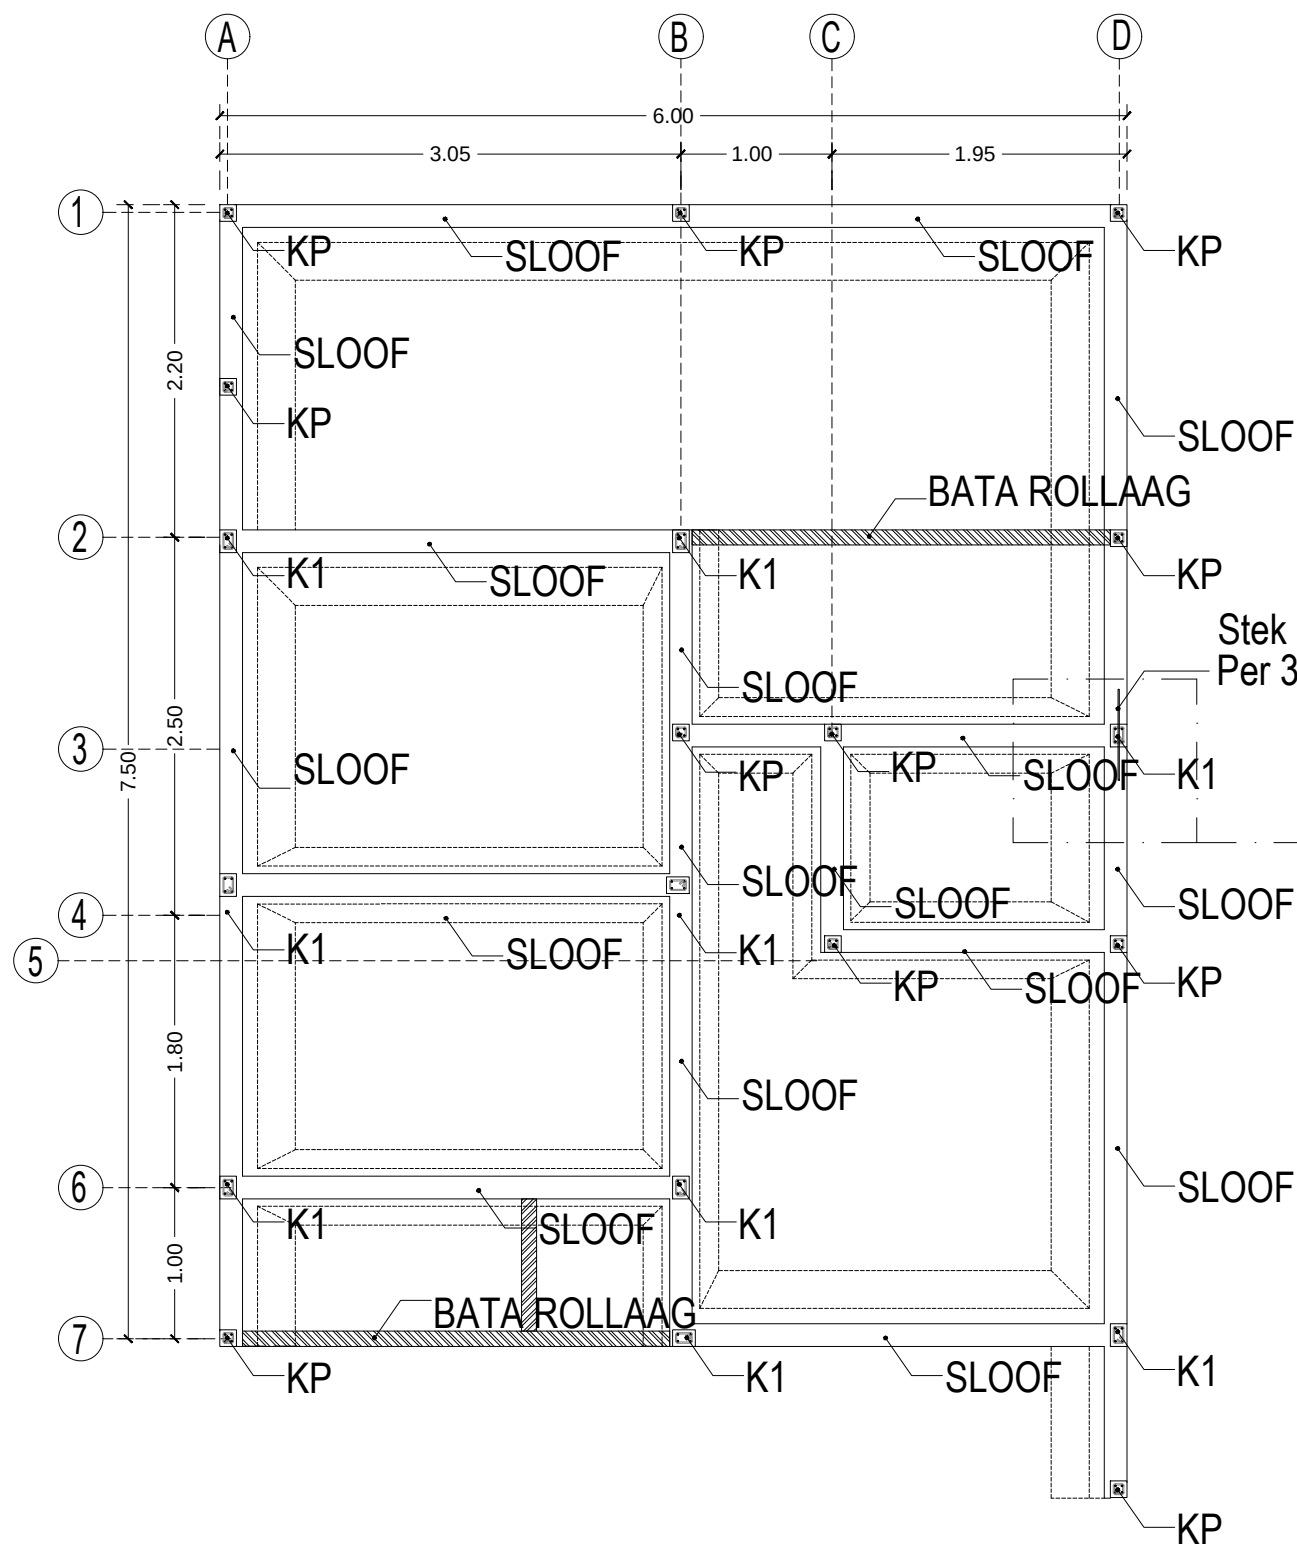

DENAH RENCANA PONDASI
Skala 1:50

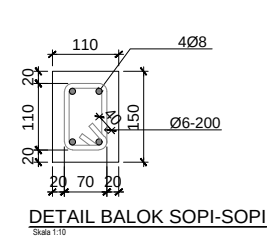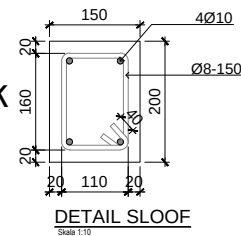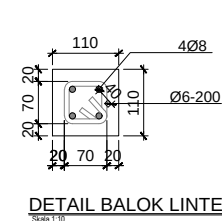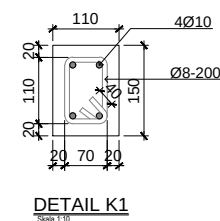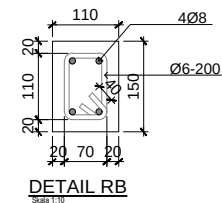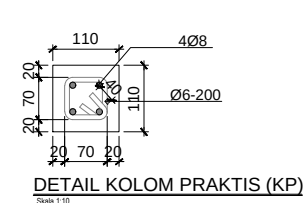

DETAIL I

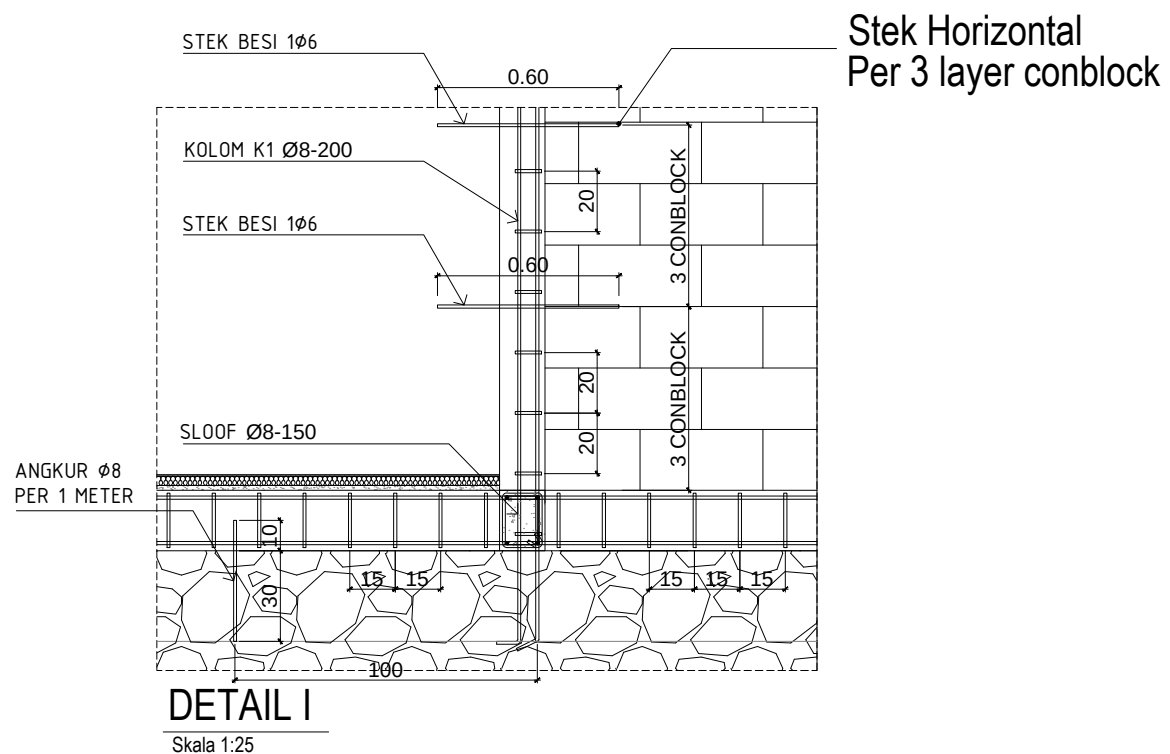

DETAIL I
Skala 1:25

CATATAN :

KETERANGAN

DEVELOPER



PT. KARYATARUNA ADHIPRATAMA
REAL ESTATE & DEVELOPER
Jalan Sukahaji No.126 Bandung 40152
Telp: (022) 82006365, 82006367 Fax: (022) 82006362

PROYEK

BUMI KARYA INDAH

GAMBAR

SKEMA STRUKTUR

TYPE 25/72 (25.2)

SKALA 1:50

DIRENCANAKAN dan DIGAMBAR :

PURNAMA KUSUMA MAHBUB

DIPERIKSA:

RANI SHINTA HAPSARI

DISETUJUI :

AGNES STEPHANIA A. T.

NO. REVISI

TANGGAL

01.

NOMOR LEMBAR



JUMLAH LEMBAR

S-08-22


24

002_PL-BKI/EX/2572-2/ASDIR/VI/2022

20/06/2022

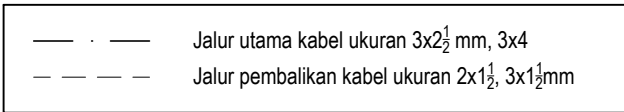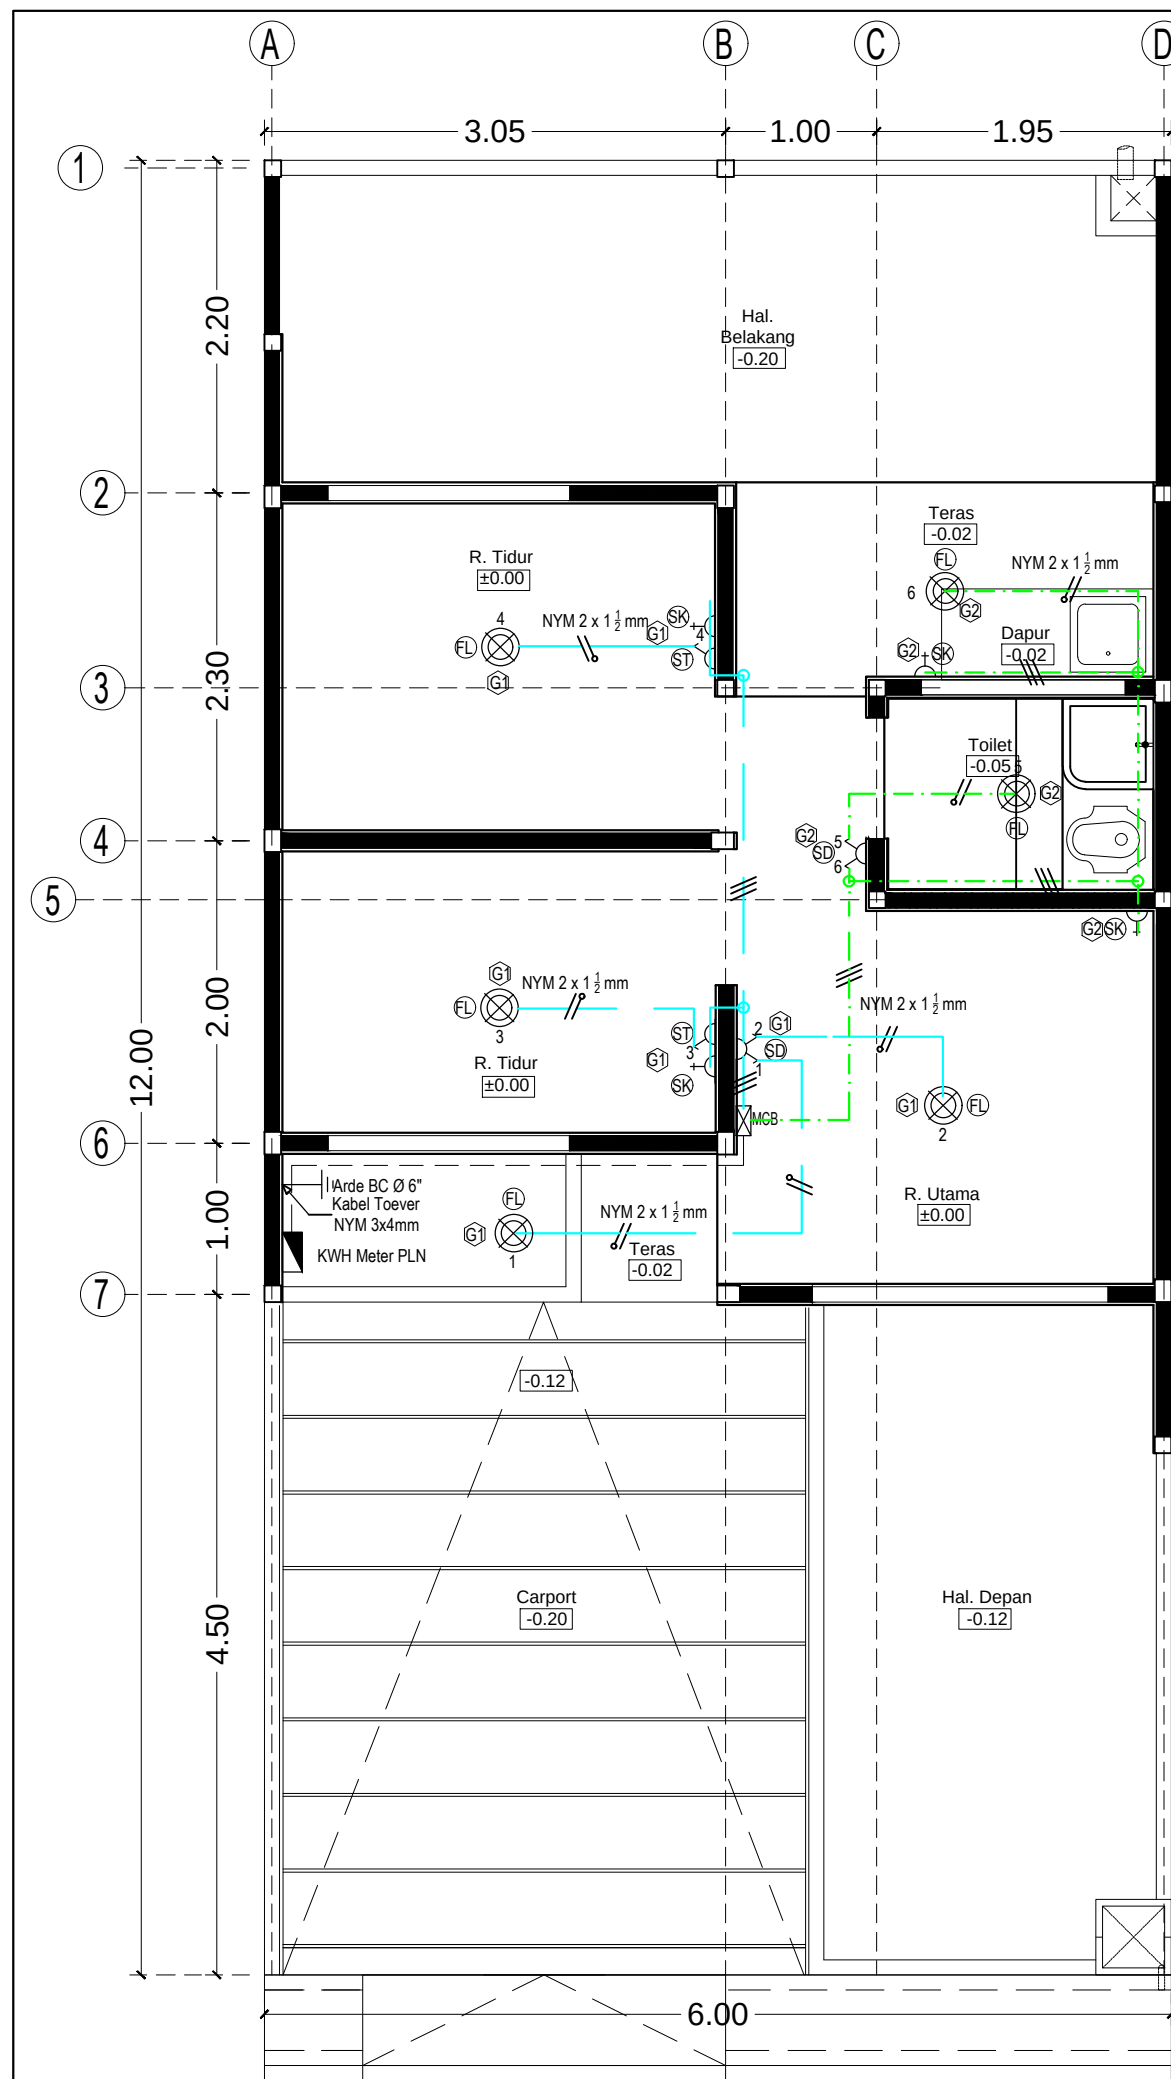

Line diagram: MCB Unit

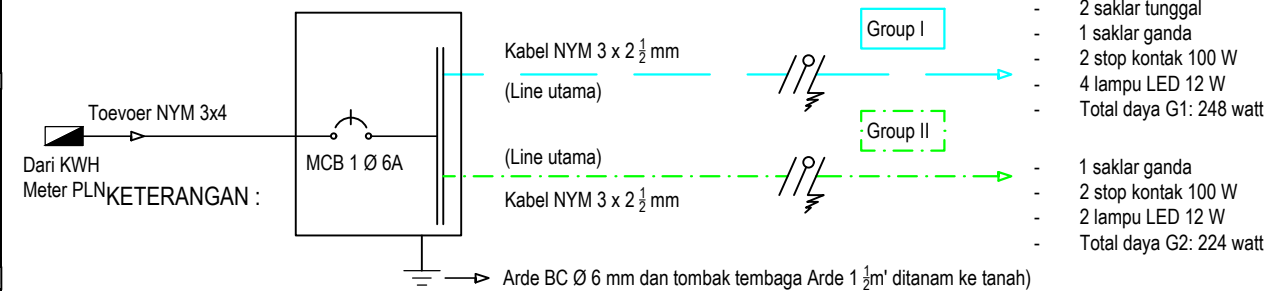

KETERANGAN :

NO GRP	TRIP AMP	6A S. TUNGGAL (ST)	6A S. GANDA (SD)	100 W S. KONTAK (SK1)	L. LED 12W F. PLAF	MCB Box	KWH Meter PLN
G1	6A	2	1	2	4	1	1
G2	6A	-	1	2	2		
JUMLAH		2	2	4	6	1	1
JUMLAH DAYA				400	72		
				472 WATT			
DAYA TERSAMBUNG PLN				900 VA			

STANDARD PEKERJAAN LISTRIK RUMAH

- Jalur utama harus pakai kabel ukuran NYM 3 x 2 $\frac{1}{2}$ mm².
- Jalur pembalikan ke titik lampu sampai ke saklar pakai kabel ukuran NYM 3 x 1 $\frac{1}{2}$, 2 x 1 $\frac{1}{2}$ mm².
- Kabel Toevoer dari Box MCB ke KWH meter PLN pakai kabel NYM 3 x 4 mm².
- Kawat arde pakai kawat BC Ø 6 mm dan tombak arde 1 $\frac{1}{2}$ m ditanam.
- Kabel-kabel listrik NYM merk Prima atau Eterna (standard PLN).
- Box MCB pakai MCB 1 Ø 6 A/10A ex. Marlin Gerin, Hager (1 group max. 15 titik stop kontak dan lampu).
- Kabel stop kontak harus pakai ukuran kabel NYM 3 x 2 $\frac{1}{2}$ mm².
- Komponen listrik : saklar, fitting lampu, stop kontak (ex. Broco standard).
- Pipa conduit Ø $\frac{5}{8}$ merk Maspion (khusus pipa listrik) warna putih.
- Tinggi stop kontak 30 cm dari lantai (Lubang stop kontak khusus pakai tutup pengaman).
- Tinggi saklar 150 cm dari lantai dan tinggi box MCB 200 cm dari lantai (di atas daun pintu teras depan/ruang tamu)

Denah Instalasi Listrik

Skala 1:50

CATATAN :

KETERANGAN

DEVELOPER



PT. KARYATARUNA ADHIPRATAMA
REAL ESTATE & DEVELOPER
Jalan Sukahaji No.126 Bandung 40152
Telp: (022) 82006365, 82006367 Fax: (022) 82006362

PROYEK

BUMI KARYA INDAH

GAMBAR

SKEMA STRUKTUR

TYPE 25/72 (25.2)

SKALA 1:50

DIRENCANAKAN dan DIGAMBAR :

PURNAMA KUSUMA MAHBUB

DIPERIKSA:

RANI SHINTA HAPSARI

DISETUJUI :

AGNES STEPHANIA A. T.

NO. REVISI

TANGGAL

01.

NOMOR LEMBAR


JUMLAH LEMBAR

ME-01-23


24

002_PL-BKI/EX/2572-2/ASDIR/VI/2022

20/06/2022

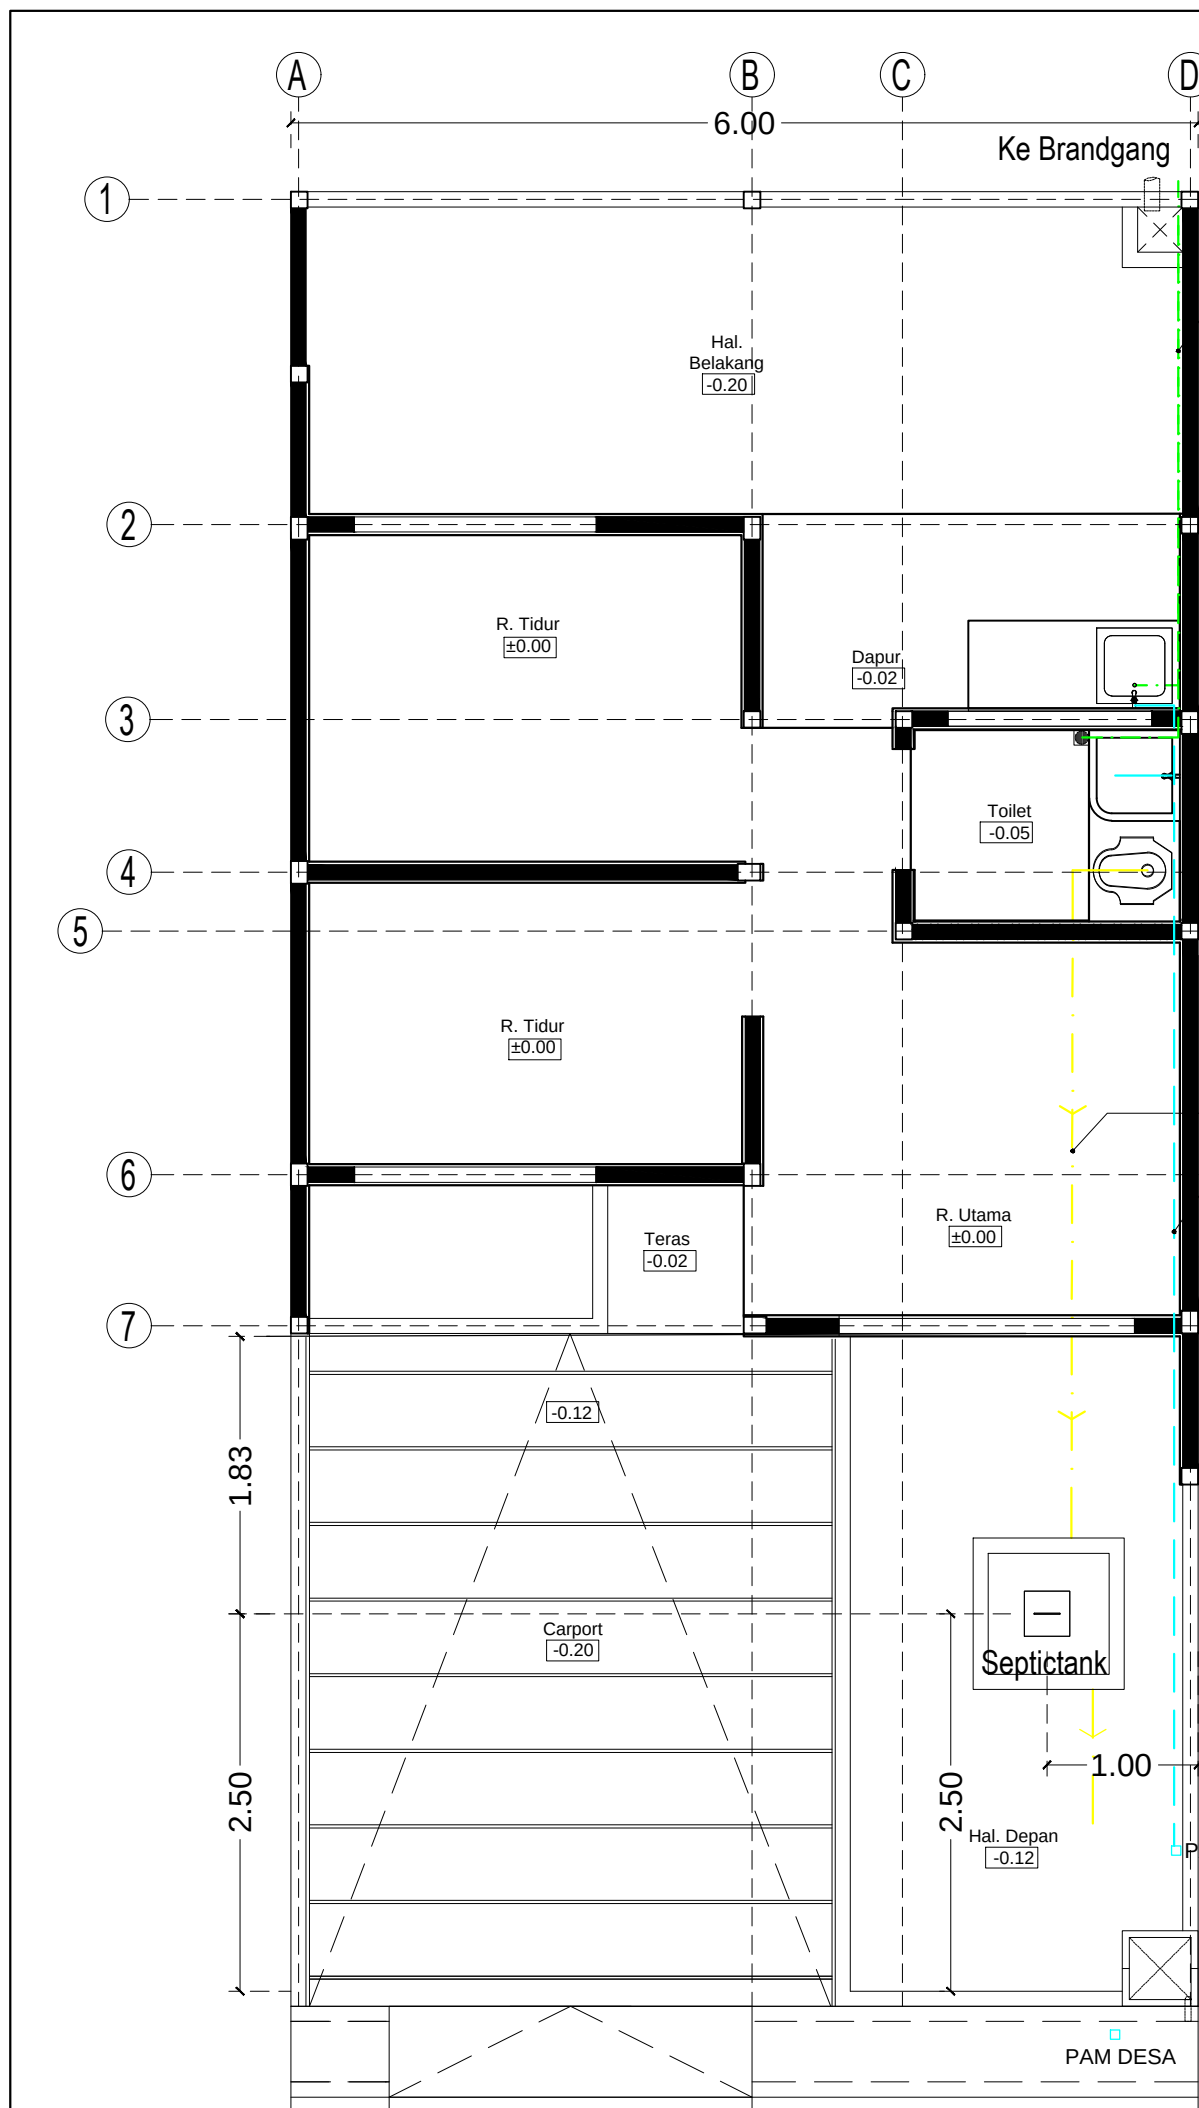

Pipa PVC Pembuangan Air 4" ke brandgang
Ex. MASPION C putih

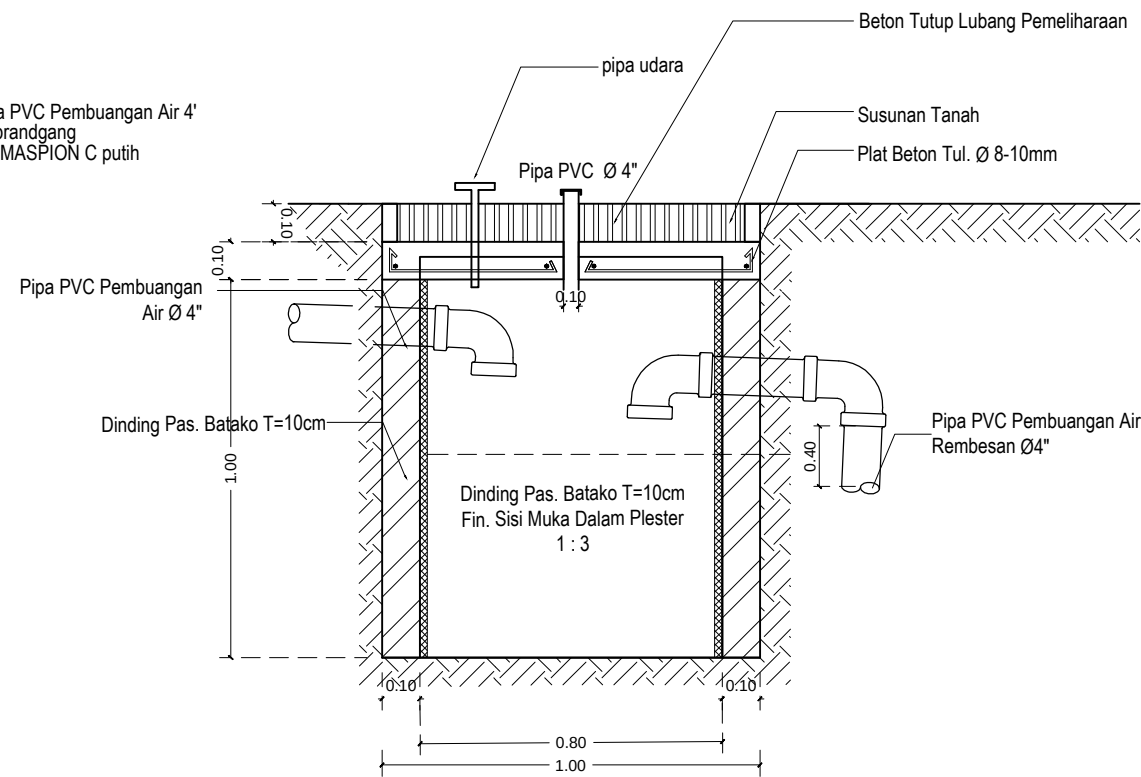


DETAIL Septictank

Skala 1:25

Pipa PVC Pembuangan Air 4" Akses Septictank
Ex. Maspion C putih uk. 4"

Pipa PVC AIR bersih dari PAM desa
AW Abu- abu 3"

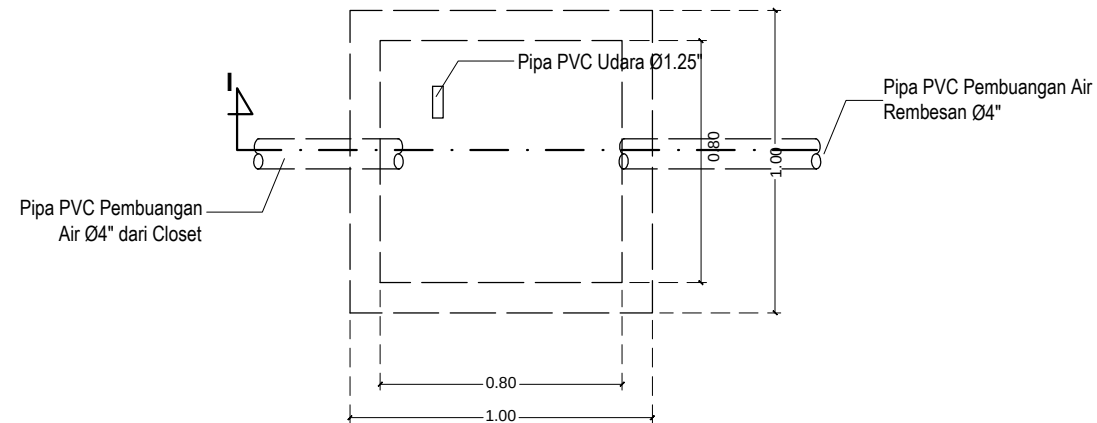

Denah Septictank

Skala 1:25

Denah Instalasi Air

Skala 1:50

CATATAN :

- KHUSUS UNTUK KEBUTUHAN GAMBAR DI LAPANGAN

KETERANGAN

- Saluran air bersih dari PAM Desa
- Saluran air pembuangan (ke Riool)
- Saluran air kotor (ke septictank)

DEVELOPER



PT. KARYATARUNA ADHIPRATAMA
REAL ESTATE & DEVELOPER
Jalan Sukahaji No.126 Bandung 40152
Telp: (022) 82006365, 82006367 Fax: (022) 82006362

PROYEK

BUMI KARYA INDAH

GAMBAR

SKEMA STRUKTUR

TYPE 25/72 (25.2)

SKALA 1:50

DIRENCANAKAN dan DIGAMBAR :

PURNAMA KUSUMA MAHBUB

DIPERIKSA:

RANI SHINTA HAPSARI

DISETUJUI :

AGNES STEPHANIA A. T.

NO. REVISI

TANGGAL

01.

NOMOR LEMBAR

JUMLAH LEMBAR

ME-02-24

24

002_PL-BKI/EX/2572-2/ASDIR/VI/2022

20/06/2022